

GRADY MEMORIAL HOSPITAL
BASE PLANS

LOCATION PLAN

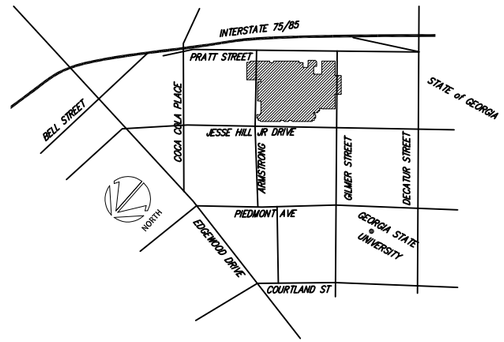

KEY PLAN

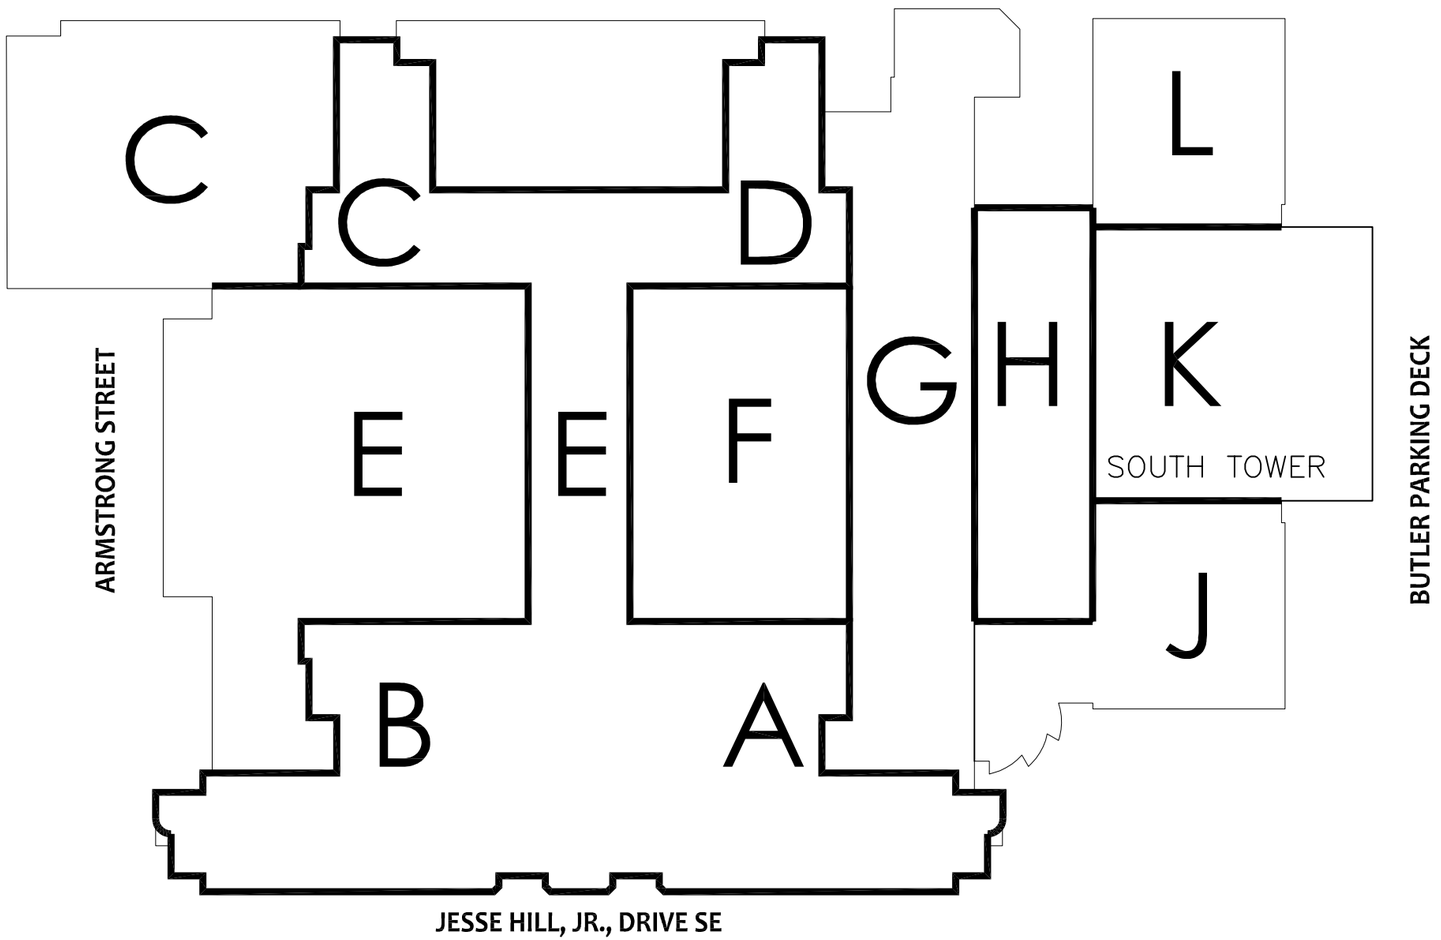

DRAWING INDEX:

GMH-0C	COVER SHEET
GMH-0S	CAMPUS SITE PLAN
GMH-0B	BASEMENT
GMH-0G	GROUND FLOOR
GMH-01	FIRST FLOOR
GMH-02	SECOND FLOOR
GMH-03	THIRD FLOOR
GMH-04	FOURTH FLOOR
GMH-05	FIFTH FLOOR
GMH-06	SIXTH FLOOR
GMH-06A	MECHANICAL FLOOR
GMH-07	SEVENTH FLOOR
GMH-08	EIGHTH FLOOR
GMH-09	NINTH FLOOR
GMH-10	TENTH FLOOR
GMH-11	ELEVENTH FLOOR
GMH-12	TWELFTH FLOOR
GMH-13	THIRTEENTH FLOOR
GMH-14	FOURTHEENTH FLOOR
GMH-15	FIFTEENTH FLOOR
GMH-16	SIXTEENTH FLOOR
GMH-MP	MECHANICAL PENTHOUSE (Floors 17 - 22)

No.	REVISION/SUBMISSION:	DATE:
1	GENERAL REVISIONS - INCLUDING SITE "CLEAN-UP"	10/14/13
2	GENERAL REVISIONS - INCLUDING SITE "CLEAN-UP"	1/18/16
3	GENERAL REVISIONS - INCLUDING "FLOOD" REBUILD	2/3/22

Grady
FACILITIES DEVELOPMENT
DEPARTMENT of FACILITIES MANAGEMENT
80 JESSE HILL, JR., DRIVE SE
ATLANTA, GEORGIA 30335
V: 404.616.4291
F: 404.616.3335

PROJECT NAME:
GRADY MEMORIAL HOSPITAL - BASE PLANS

PROJECT LOCATION:
GRADY MEMORIAL HOSPITAL
80 JESSE HILL, JR., DRIVE SE
ATLANTA, GEORGIA 30303

PN: N/A
SCALE: NOT TO SCALE
DRAWN BY: GCS3
DATE: 3/30/11

DRAWING TITLE: BASEMENT
APPROVALS:
SHEET NUMBER: GMH-0C

NOT FOR CONSTRUCTION



Grady
FACILITIES DEVELOPMENT
DEPARTMENT of FACILITIES MANAGEMENT
80 JESSE HILL, JR., DRIVE SE
ATLANTA, GEORGIA 30335
V: 404.616.4291
F: 404.616.3355

PROJECT NAME:
GRADY MEMORIAL HOSPITAL - BASE PLANS


PROJECT LOCATION:
BASEMENT FLOOR PLAN
80 JESSE HILL, JR., DRIVE SE
ATLANTA, GEORGIA 30303

No.	REVISION/SUBMISSION:	DATE:
1	GENERAL REVISIONS - CART WASH / PROBE CLEANING	10/14/13
2	GENERAL REVISIONS - C.E.D. // INPATIENT PHARMACY // E.D.	1/18/16
3	MAIN INPATIENT PHARMACY U.S.P. 800 REMODELING	PENDING

PN: N/A
SCALE: NTS
DRAWN BY: GCS3
DATE: 3/30/11

DRAWING TITLE: GROUND FLOOR
APPROVALS:
SHEET NUMBER: GMH-B

NOT FOR CONSTRUCTION

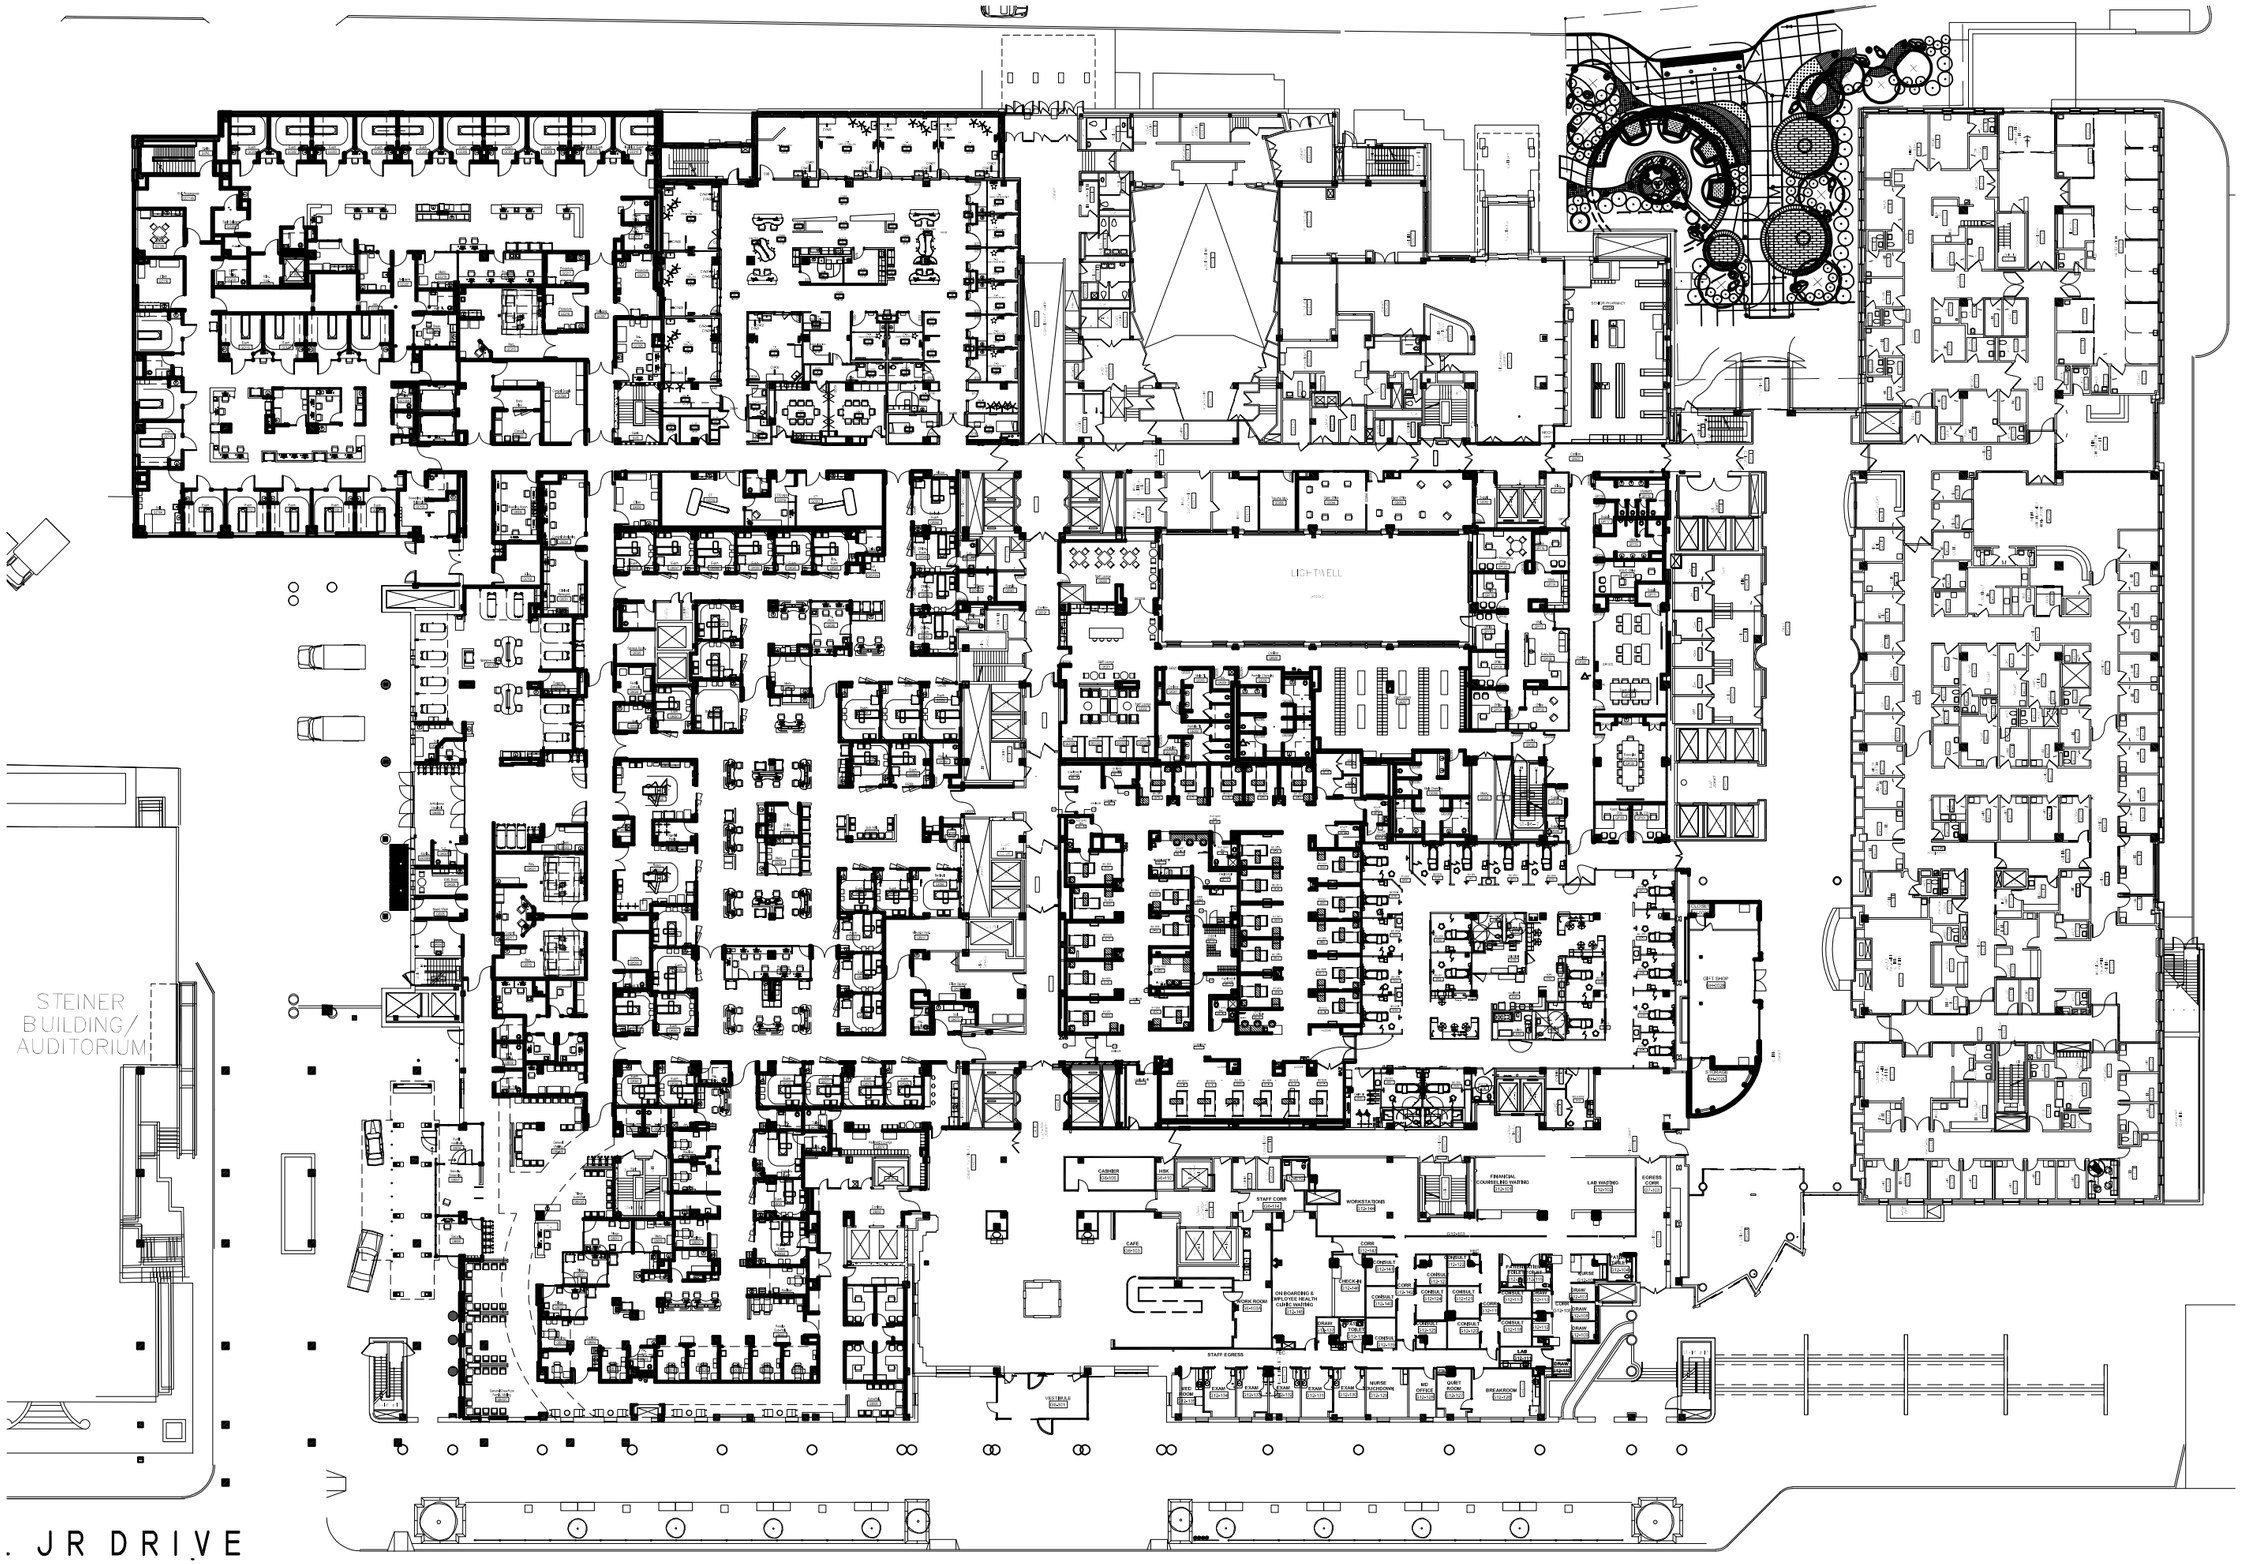

Grady
DEPARTMENT of FACILITIES MANAGEMENT
80 JESSE HILL, JR., DRIVE SE
ATLANTA, GEORGIA 30335
V: 404.616.4291
F: 404.616.3335


PROJECT NAME:
GRADY MEMORIAL HOSPITAL BASE PLANS

PROJECT LOCATION:
GROUND FLOOR
80 JESSE HILL, JR., DRIVE SE
ATLANTA, GEORGIA 30303

PN:	N/A
SCALE:	NTS
DRAWN BY:	gcs3
DATE:	2/3/22

DRAWING TITLE:	STAIR NUMBERS
APPROVALS:	
SHEET NUMBER:	GMH-G


NOT FOR CONSTRUCTION

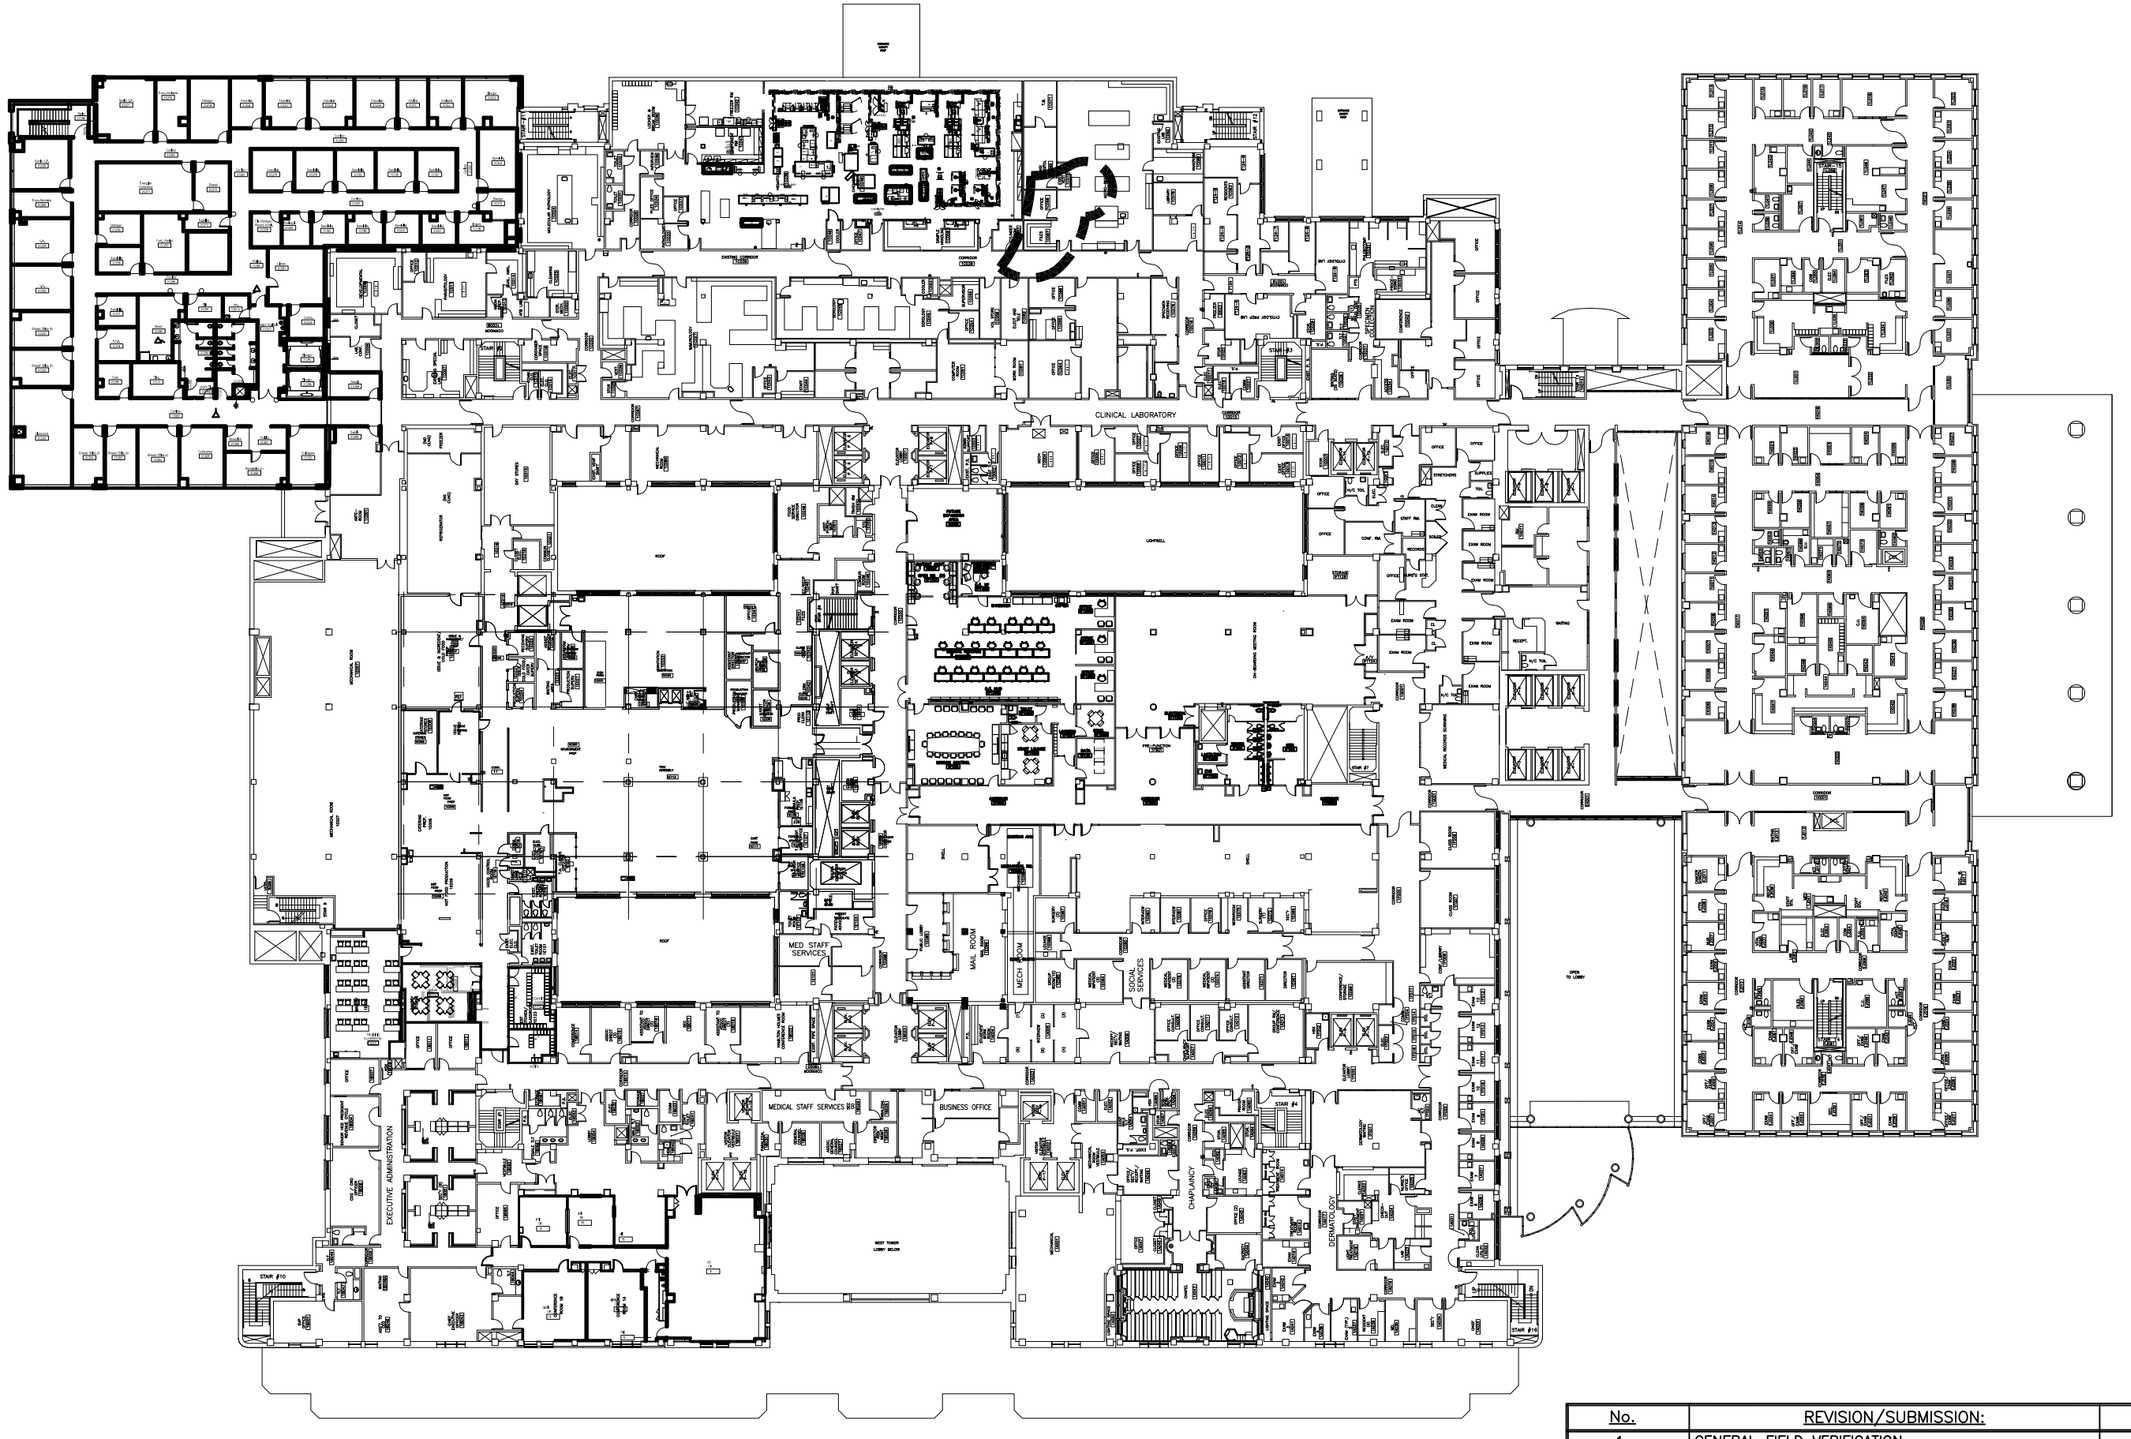

No.	REVISION/SUBMISSION:	DATE:
1	GENERAL FIELD VERIFICATION	3/16/12
2	BOARD ROOM/CARE LOGISTICS/KITCHEN UPGRADES	1/6/22

Grady
DEPARTMENT of FACILITIES MANAGEMENT
80 JESSE HILL, JR., DRIVE SE
ATLANTA, GEORGIA 30335
V: 404.616.4291
F: 404.616.3335

KEY PLAN

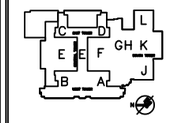


PROJECT NAME:
GRADY MEMORIAL HOSPITAL – BASE FLOOR PLANS

PROJECT LOCATION:
GRADY MEMORIAL HOSPITAL
80 JESSE HILL, JR., DRIVE SE
ATLANTA, GEORGIA 30303

PN: N/A
SCALE: NOT TO SCALE
DRAWN BY: gc53
DATE: 3/30/11

DRAWING TITLE: FIRST FLOOR
APPROVALS:
SHEET NUMBER: GMH-01

NOT FOR CONSTRUCTION

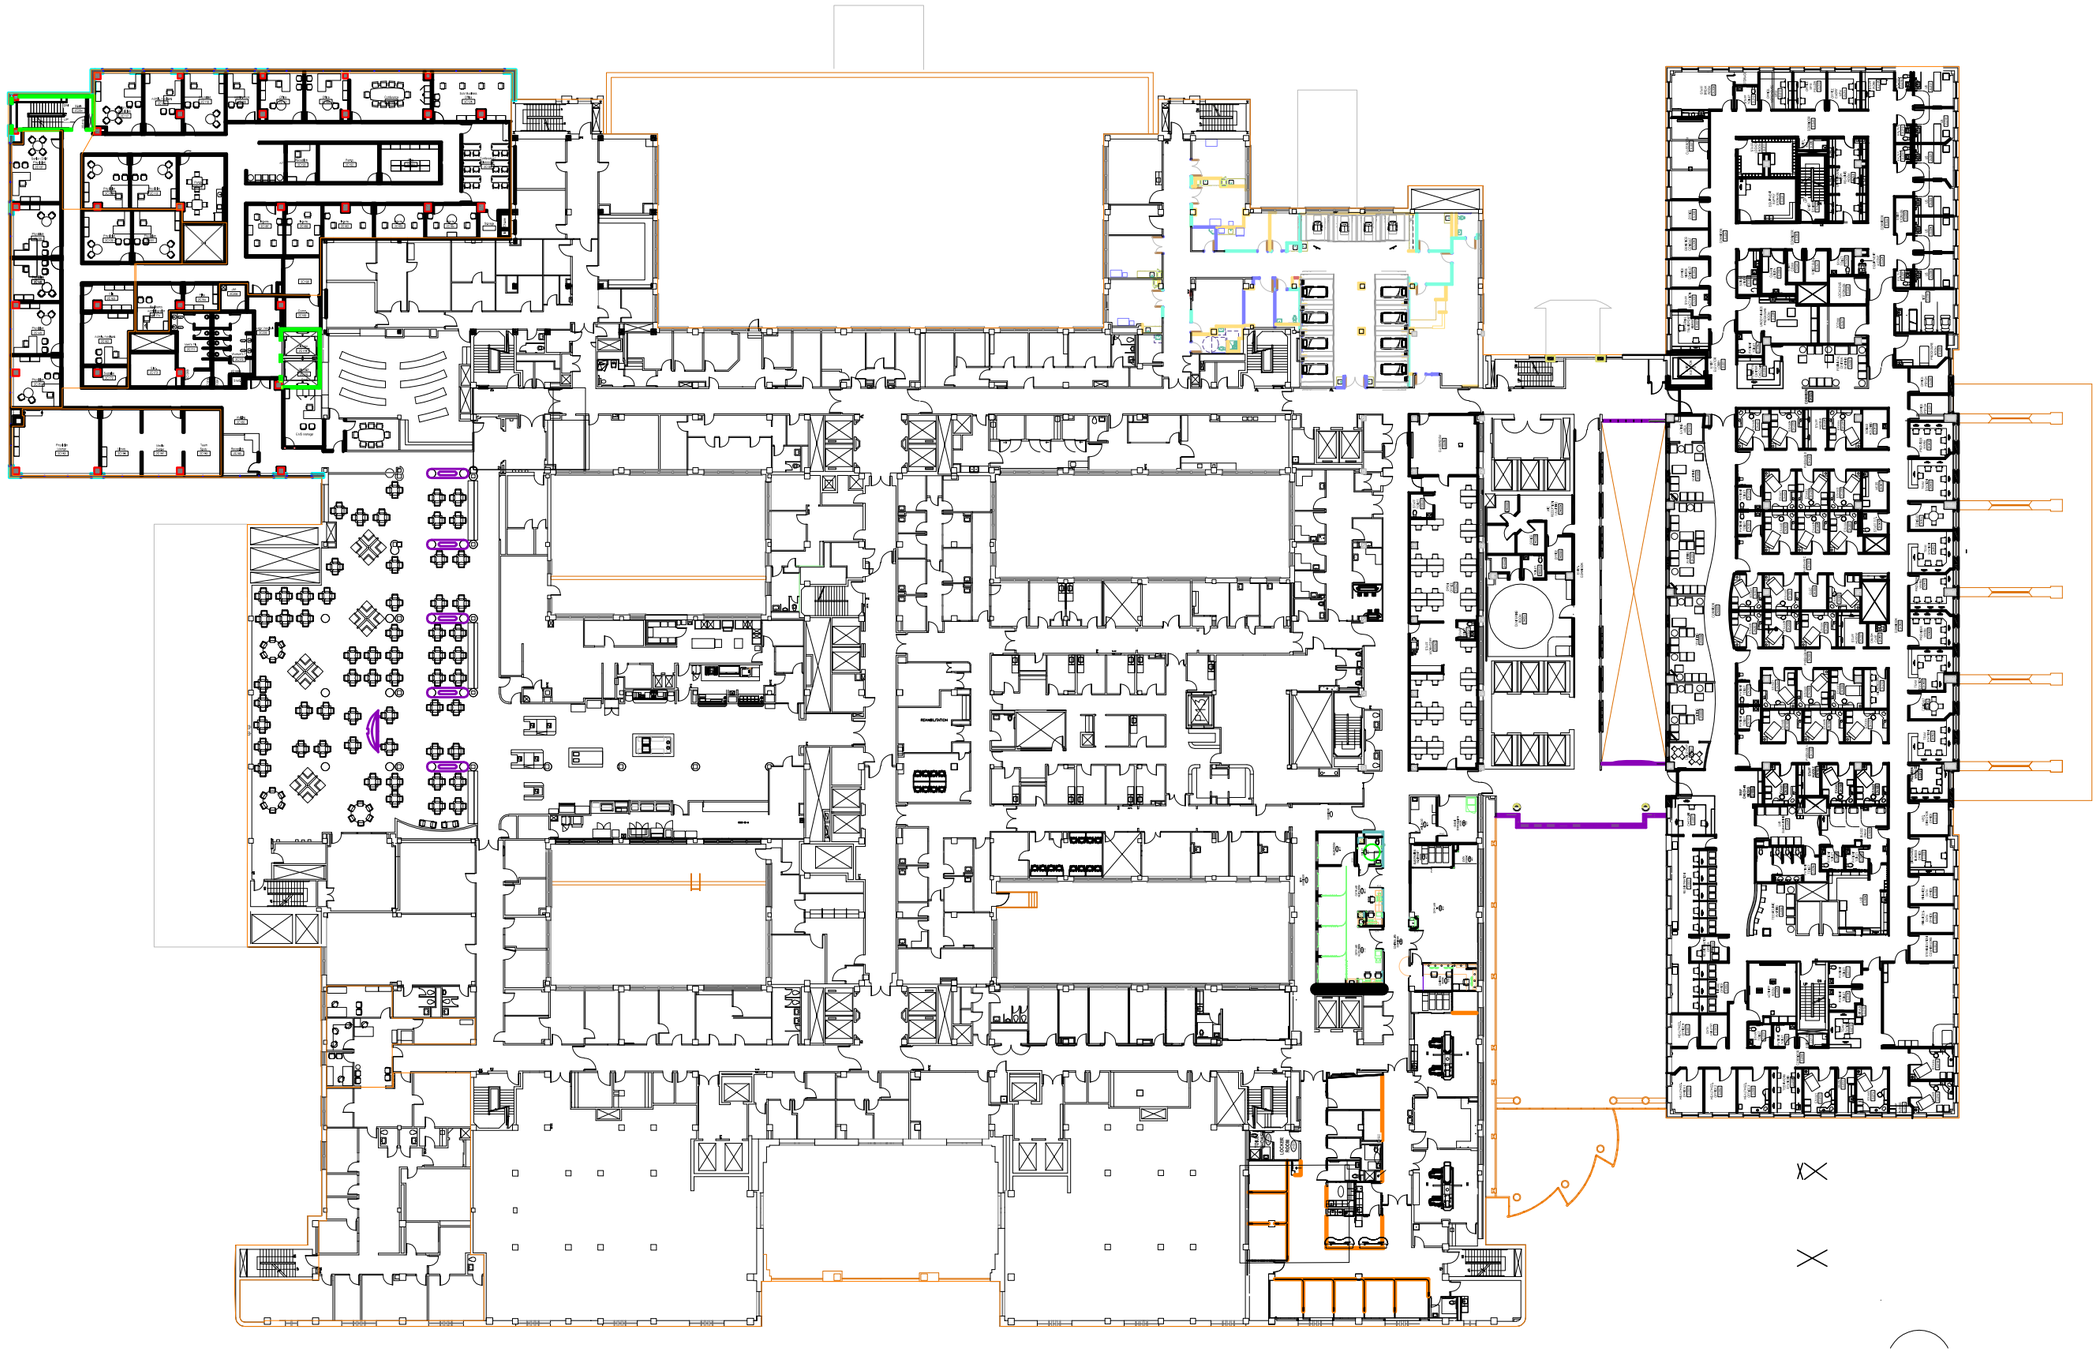

No.	REVISION/SUBMISSION:	DATE:
1	GENERAL BACKGROUND UPDATE	3/16/12
2	CORRELL CARDIAC CENTER REVISION	10/14/13
3	GI RENOVATION / CAFETERIA SERVERY / ED EXPANSION	1/15/16
4	NURSING ADMINISTRATION	2/24/17
5	CATH LAB 3	2/17/22

Grady
DEPARTMENT of FACILITIES MANAGEMENT
80 JESSE HILL, JR., DRIVE SE
ATLANTA, GEORGIA 30335
V: 404.616.4291
F: 404.616.3335


PROJECT NAME:
GRADY MEMORIAL HOSPITAL – BASE PLANS

PROJECT LOCATION:
SECOND FLOOR
80 JESSE HILL, JR., DRIVE SE
ATLANTA, GEORGIA 30303

PN: TBD
SCALE: NTS
DRAWN BY: GCS3
DATE: 7/21/11

DRAWING TITLE: SECOND FLOOR
APPROVALS:
SHEET NUMBER: GMH-02

NOT FOR CONSTRUCTION

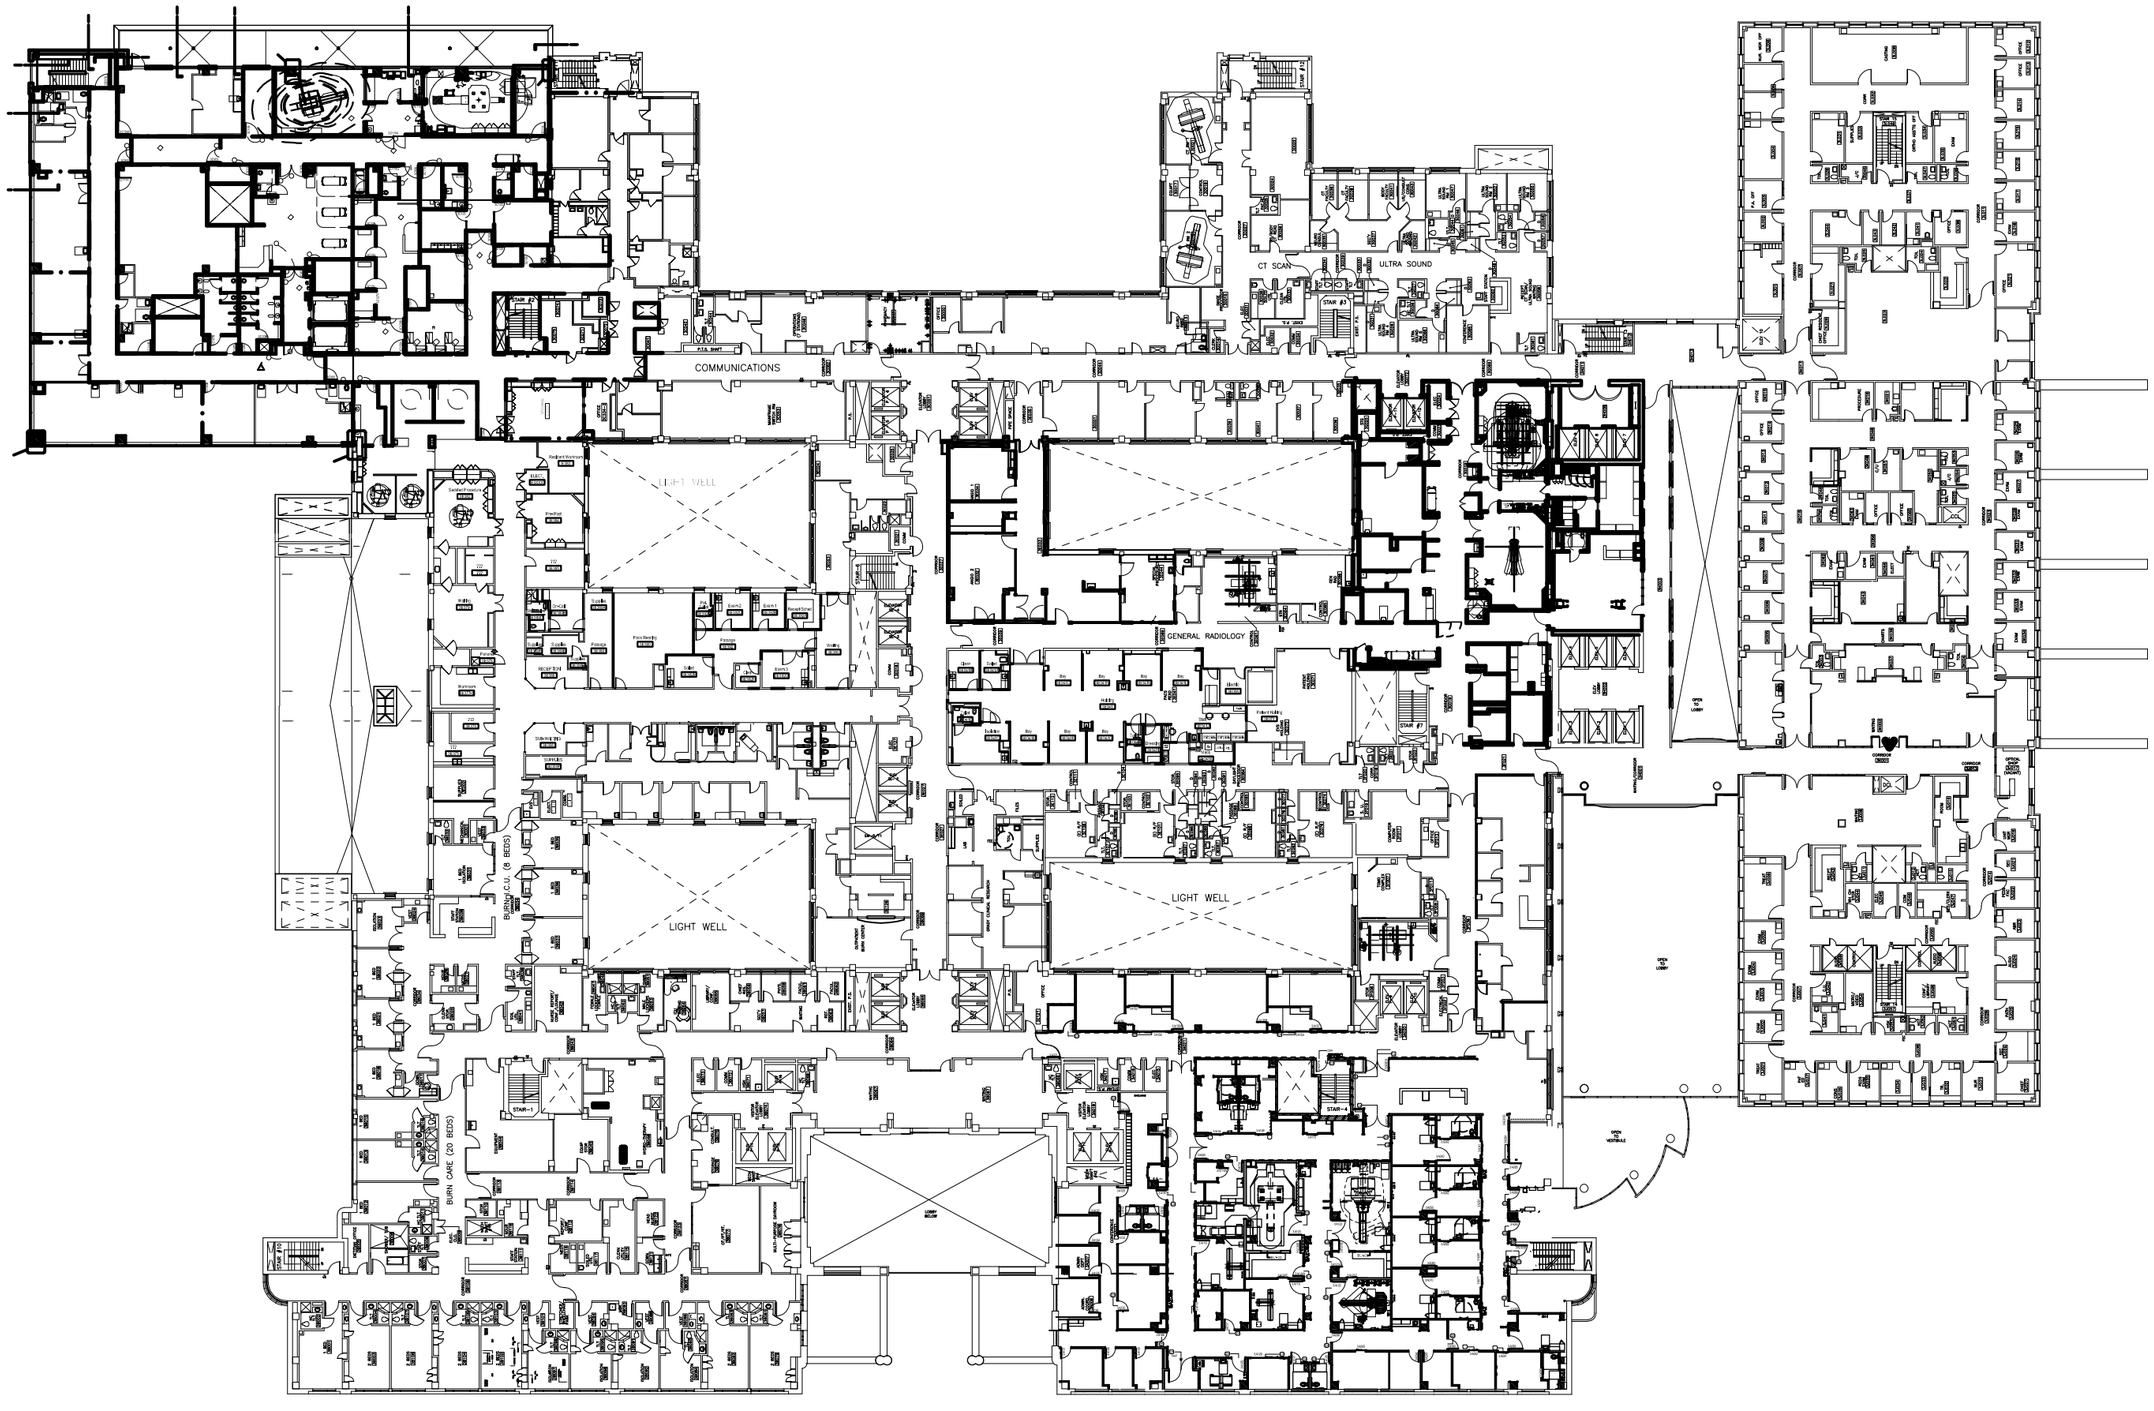

Grady

DEPARTMENT of FACILITIES MANAGEMENT
80 JESSE HILL, JR., DRIVE SE
ATLANTA, GEORGIA 30335
V: 404.616.4291
F: 404.616.3335

KEY PLAN

PROJECT NAME:
GRADY MEMORIAL HOSPITAL BASE PLANS

PROJECT LOCATION:
THIRD FLOOR
80 JESSE HILL, JR., DRIVE SE
ATLANTA, GEORGIA 30303

PN: N/A

SCALE: NOT TO SCALE

DRAWN BY: gc53

DATE: 3/30/11

No.	REVISION/SUBMISSION:	DATE:
1	GENERAL REVISIONS	3/17/12
2	PATIENT ELEGIBILITY (CORRELL CARDIAC RELOCATION)	8/8/13
3	CLINICAL RESEARCH / BURN UNIT FIELD VERIFICATION	7/8/15
4	ED EXPANSION / INPATIENT MRI	1/29/16
5	3-A FLOOD REBUILD / MRI-1 / IR & X-RAY RELOCATION/ED U-S	1/24/22

DRAWING TITLE: THIRD FLOOR

APPROVALS:

SHEET NUMBER: GMH-03

NOT FOR CONSTRUCTION

Grady
DEPARTMENT of FACILITIES MANAGEMENT
80 JESSE HILL, JR., DRIVE SE
ATLANTA, GEORGIA 30335
V: 404.616.4291
F: 404.616.3335

– BASE PLANS

PROJECT NAME:
GRADY MEMORIAL HOSPITAL


PROJECT LOCATION:
FOURTH FLOOR
80 JESSE HILL, JR. DRIVE SE
ATLANTA, GEORGIA 30303

PN:	10115
SCALE:	NTS
DRAWN BY:	gcs3
DATE:	7/21/11

DRAWING TITLE:	FOURTH FLOOR
GSF:	143,110 GSF
SHEET NUMBER:	GMH-04

NOT FOR CONSTRUCTION


No.	REVISION/SUBMISSION:	DATE:
1	4-A/4-B FLOOD REBUILD	1/24/22

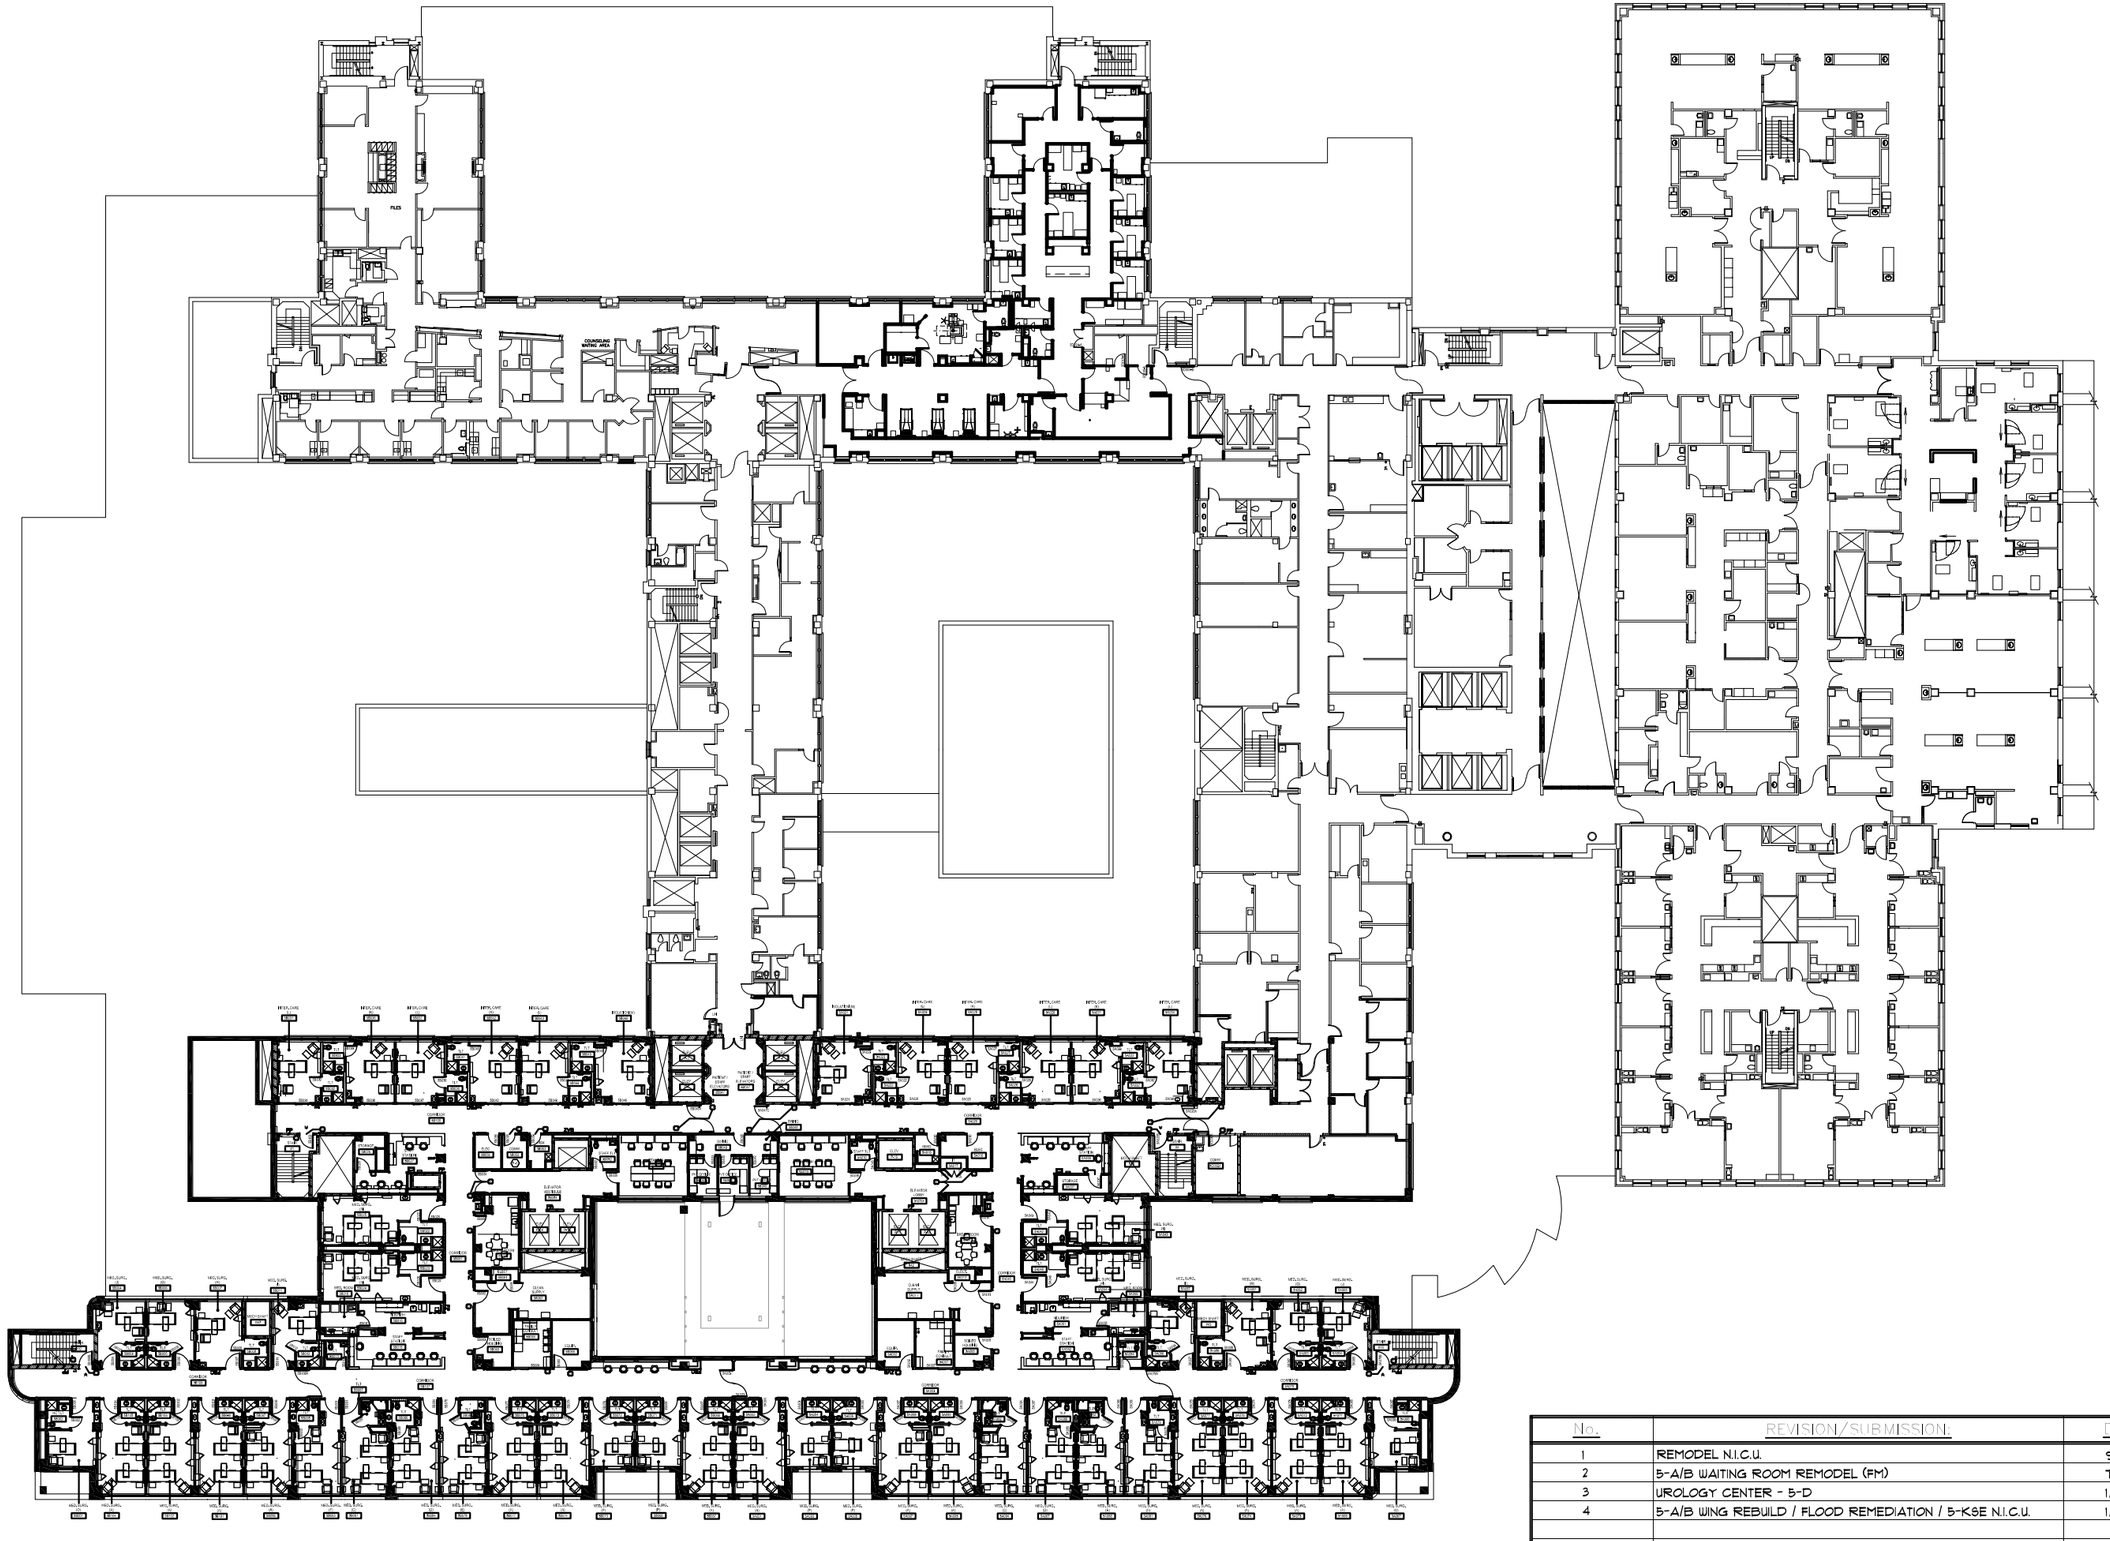

Grady
FACILITIES DEVELOPMENT

DEPARTMENT of FACILITIES MANAGEMENT
80 JESSE HILL, JR., DRIVE SE
ATLANTA, GEORGIA 30335
V: 404.616.4291
F: 404.616.3355

KEY PLAN

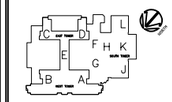

PROJECT NAME:
GRADY MEMORIAL HOSPITAL - BASE FLOOR PLANS

PROJECT LOCATION:
FIFTH FLOOR
80 JESSE HILL, JR., DRIVE SE
ATLANTA, GEORGIA 30303

PN: N/A
SCALE: NOT TO SCALE
DRAWN BY: gcs3
DATE: 7/21/11

No.	REVISION/SUBMISSION:	DATE:
1	REMODEL N.I.C.U.	9/14/12
2	5-A/B WAITING ROOM REMODEL (FM)	7/30/14
3	UROLOGY CENTER - 5-D	1/15/16
4	5-A/B WING REBUILD / FLOOD REMEDIATION / 5-K&E N.I.C.U.	1/4/22

DRAWING TITLE: FIFTH FLOOR
APPROVALS:
SHEET NUMBER: **GMH-05**

NOT FOR CONSTRUCTION



Grady
DEPARTMENT of FACILITIES MANAGEMENT
80 JESSE HILL, JR., DRIVE SE
ATLANTA, GEORGIA 30335
V: 404.616.4291
F: 404.616.3355

PROJECT NAME:
GRADY MEMORIAL HOSPITAL - BASE FLOOR PLANS


PROJECT LOCATION:
GRADY MEMORIAL HOSPITAL
80 JESSE HILL, JR., DRIVE SE
ATLANTA, GEORGIA 30303

No.	REVISION/SUBMISSION:	DATE:
1	GENERAL UPDATED - HYBRID OR / 6-A & 6-B FLOOD REMEDIATION	1/21/22

PN: 11118
SCALE: NOT TO SCALE
DRAWN BY: gcs3
DATE: 7/21/11


DRAWING TITLE: SIXTH FLOOR
APPROVALS:
SHEET NUMBER: GMH-06

NOT FOR CONSTRUCTION

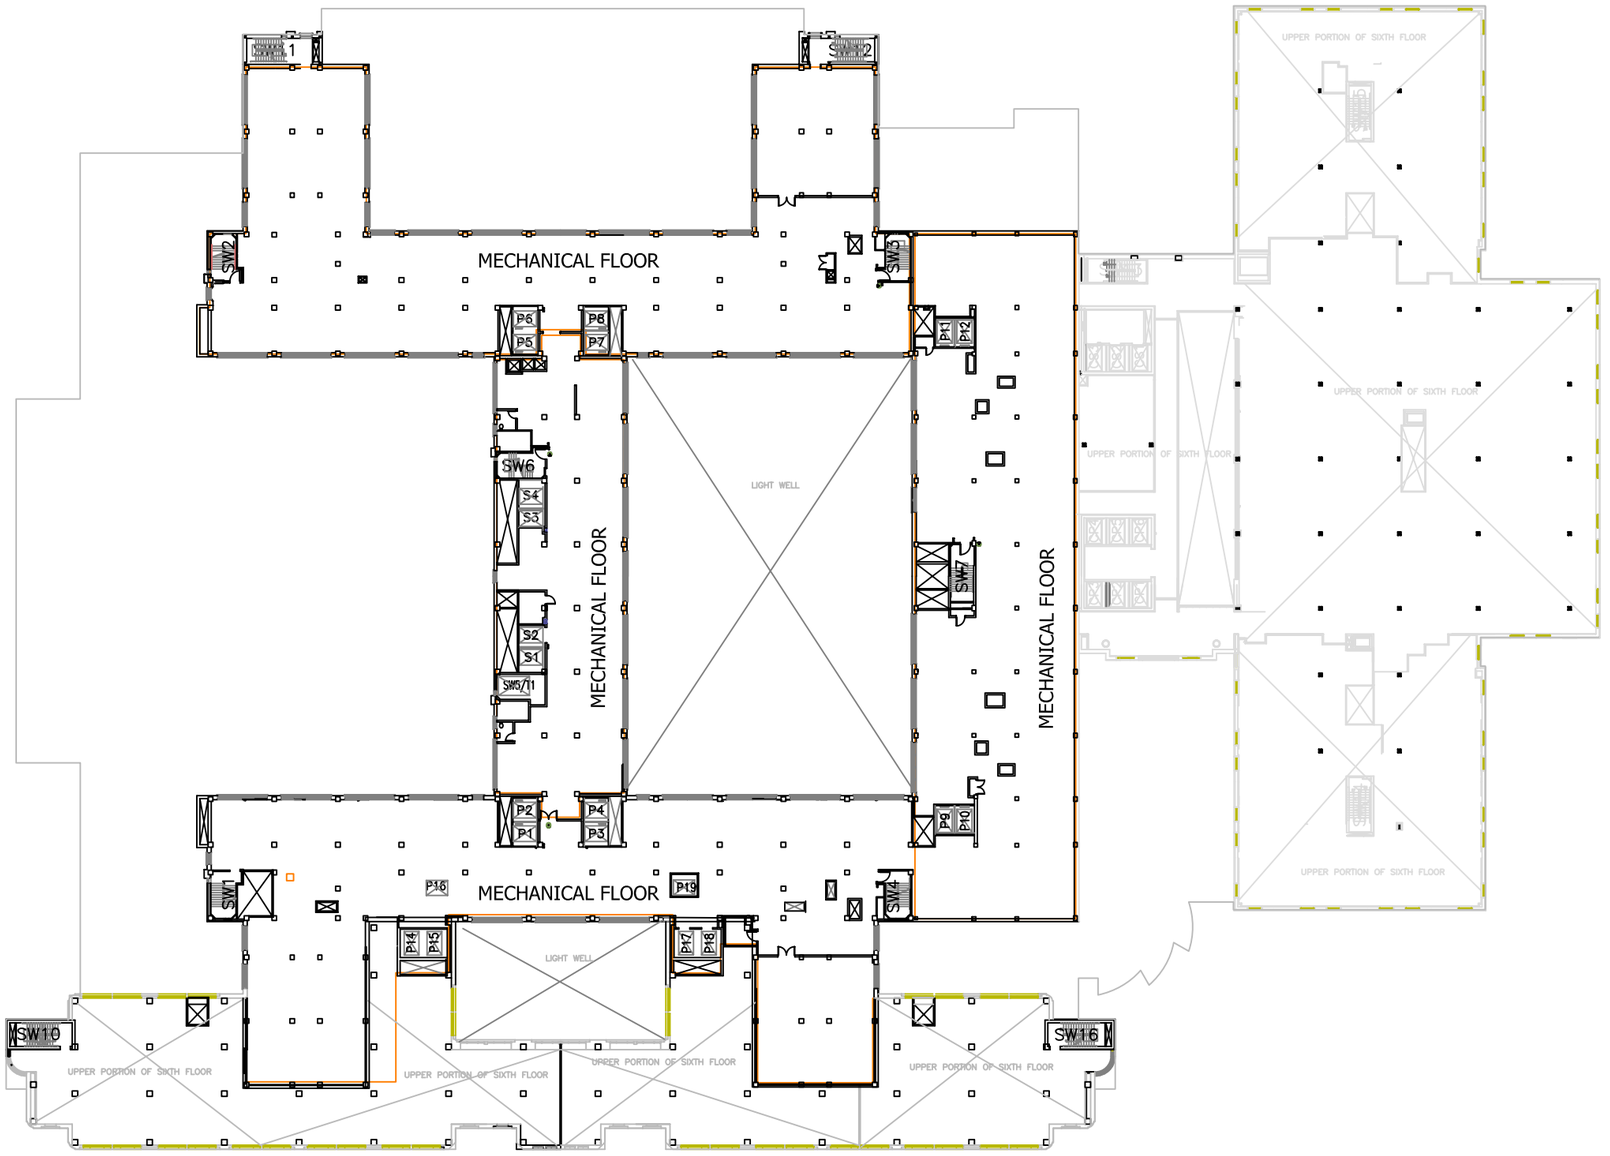

No.	Revisions/Submissions	Date

Key Plan:

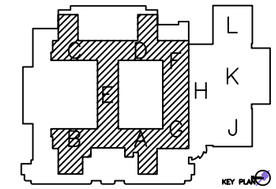

Project Title:

DEPARTMENT LOCATIONS
GRADY MEMORIAL HOSPITAL

80 JESSE HILL, JR, DRIVE SE
ATLANTA, GEORGIA 30303


Grady Health System
Department of Facilities Development

80 Jesse Hill, Jr., Drive SE
Atlanta, Georgia 30335
404/616-4291

Location:
80 JESSE HILL, JR, DRIVE SE
ATLANTA, GEORGIA 30303

Drawing Title:
MECHANICAL FLOOR PLAN

Drawn by:	GHS Project No.:
gcs3	N/A
Reviewed by:	Scale:
	NTS
Approved by:	Drawing Number:
Date: 12/4/06	GMH-06A

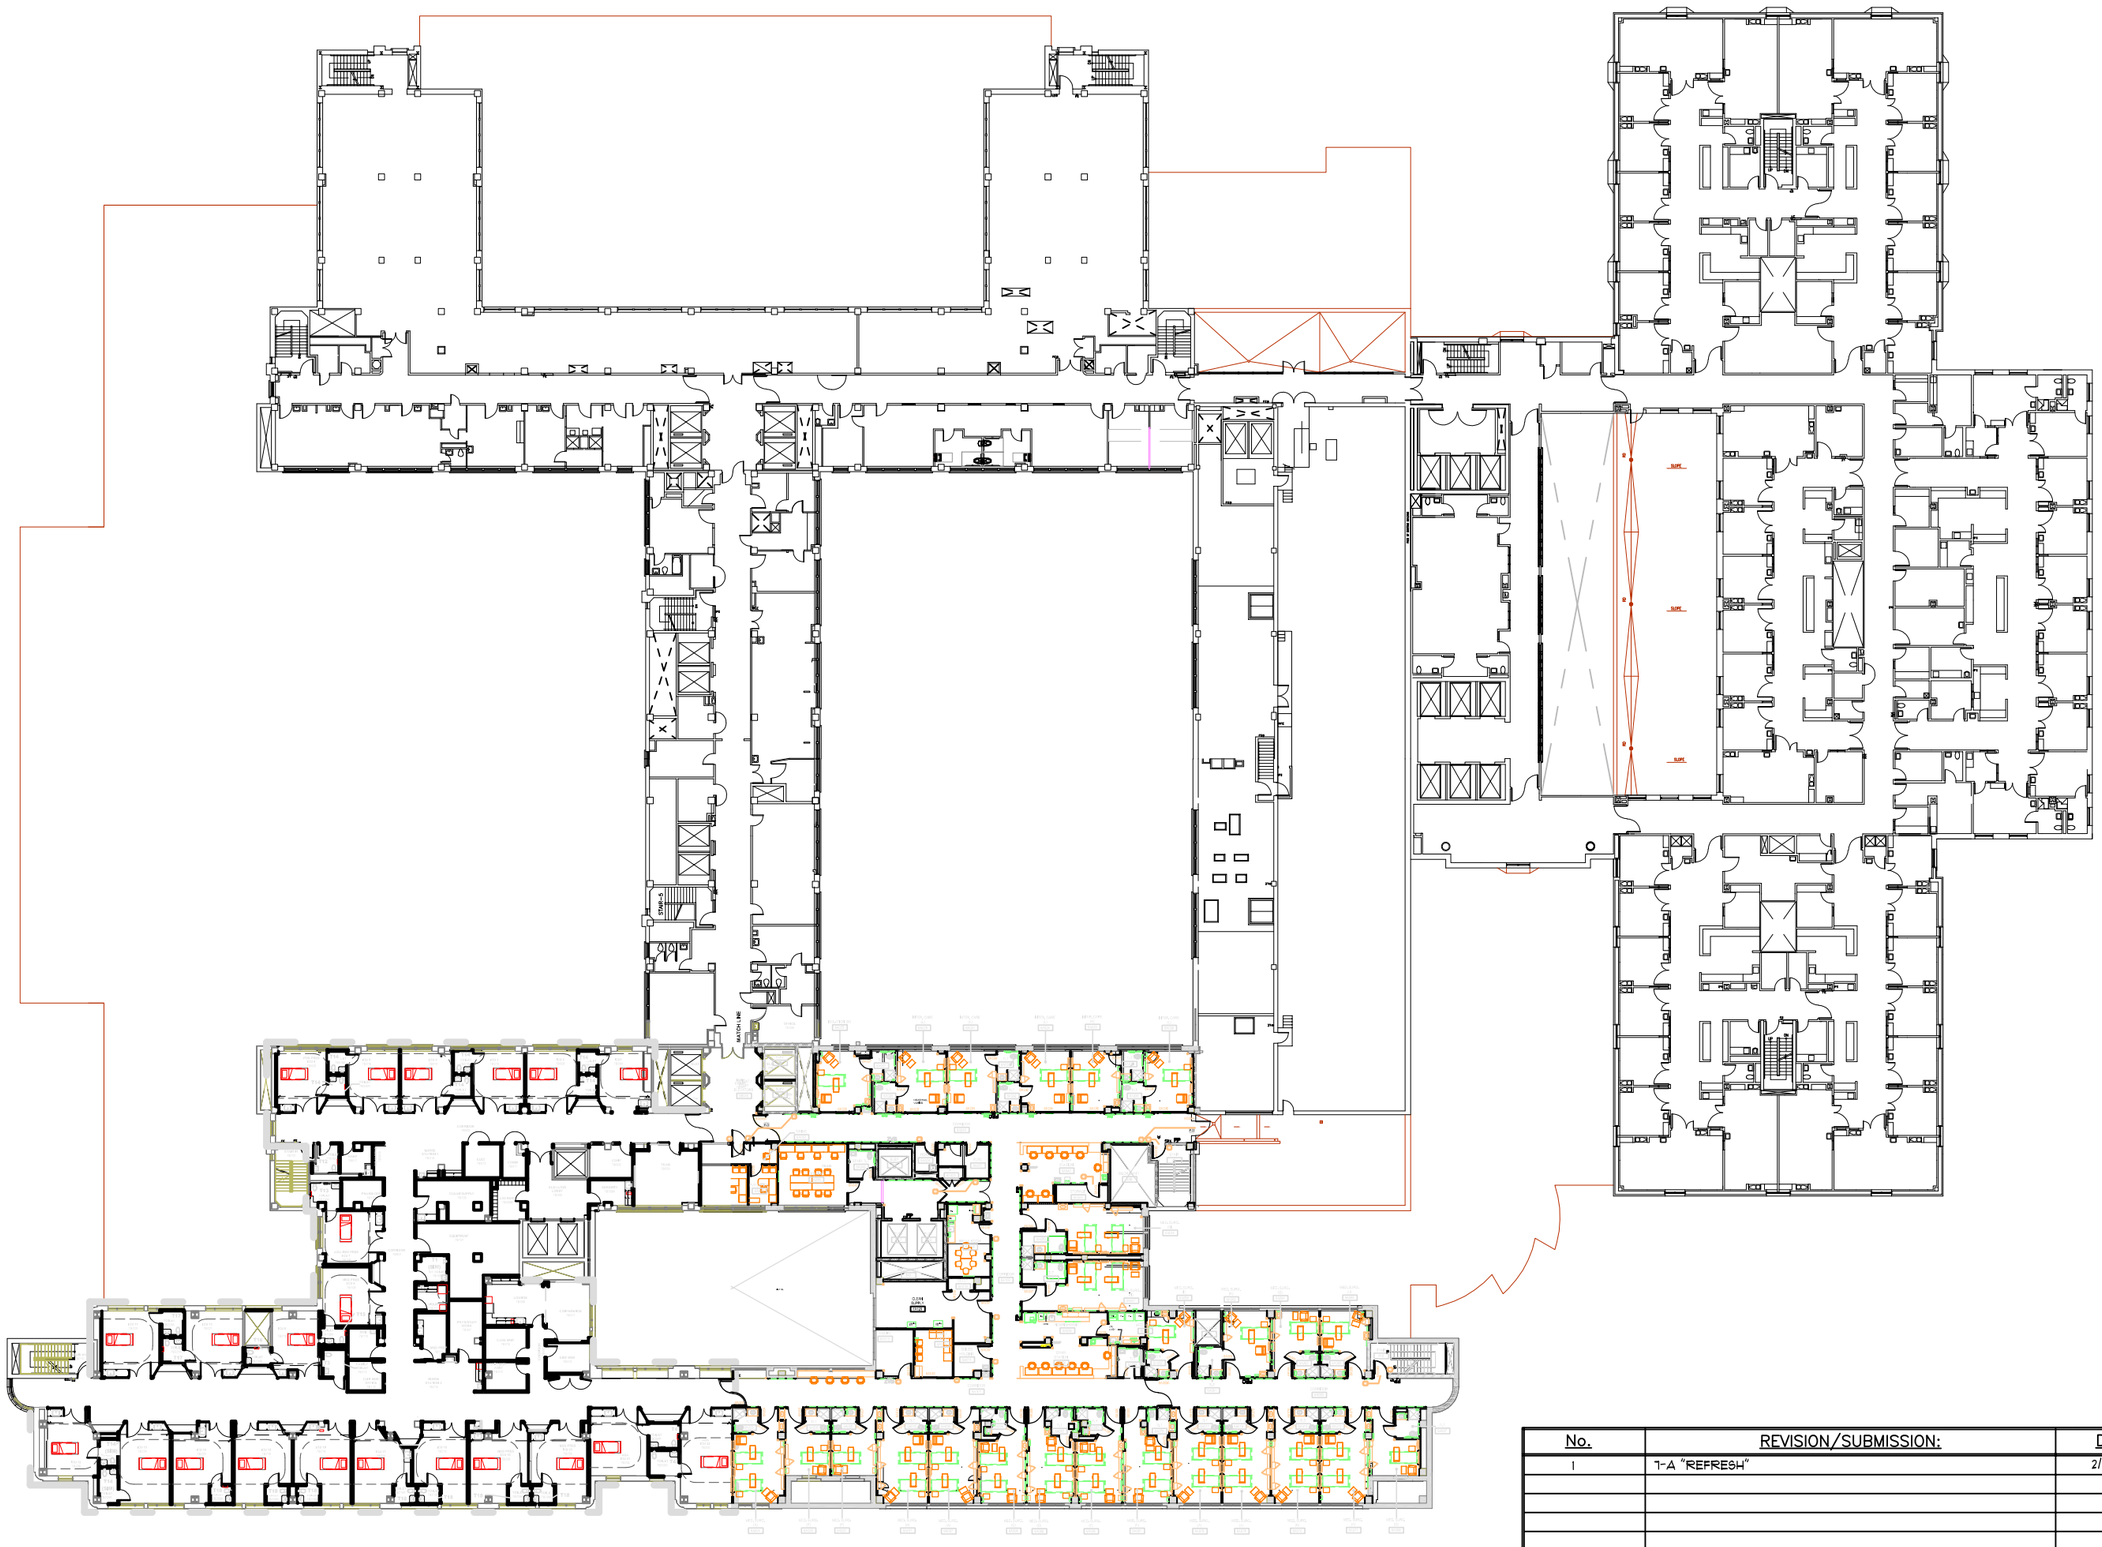

Grady

DEPARTMENT of FACILITIES MANAGEMENT

80 JESSE HILL, JR., DRIVE SE

ATLANTA, GEORGIA 30335

V: 404.616.4291

F: 404.616.3335

PROJECT NAME:
GRADY MEMORIAL HOSPITAL – BASE PLANS

PROJECT LOCATION:
SEVENTH FLOOR
80 JESSE HILL, JR., DRIVE SE
ATLANTA, GEORGIA 30303

PN:	N/A
SCALE:	NOT TO SCALE
DRAWN BY:	gcs3
DATE:	3/30/11


No.	REVISION/SUBMISSION:	DATE:
1	7-A "REFRESH"	2/1/22

DRAWING TITLE:
SEVENTH FLOOR

APPROVALS:

SHEET NUMBER:
GMH-07

NOT FOR CONSTRUCTION

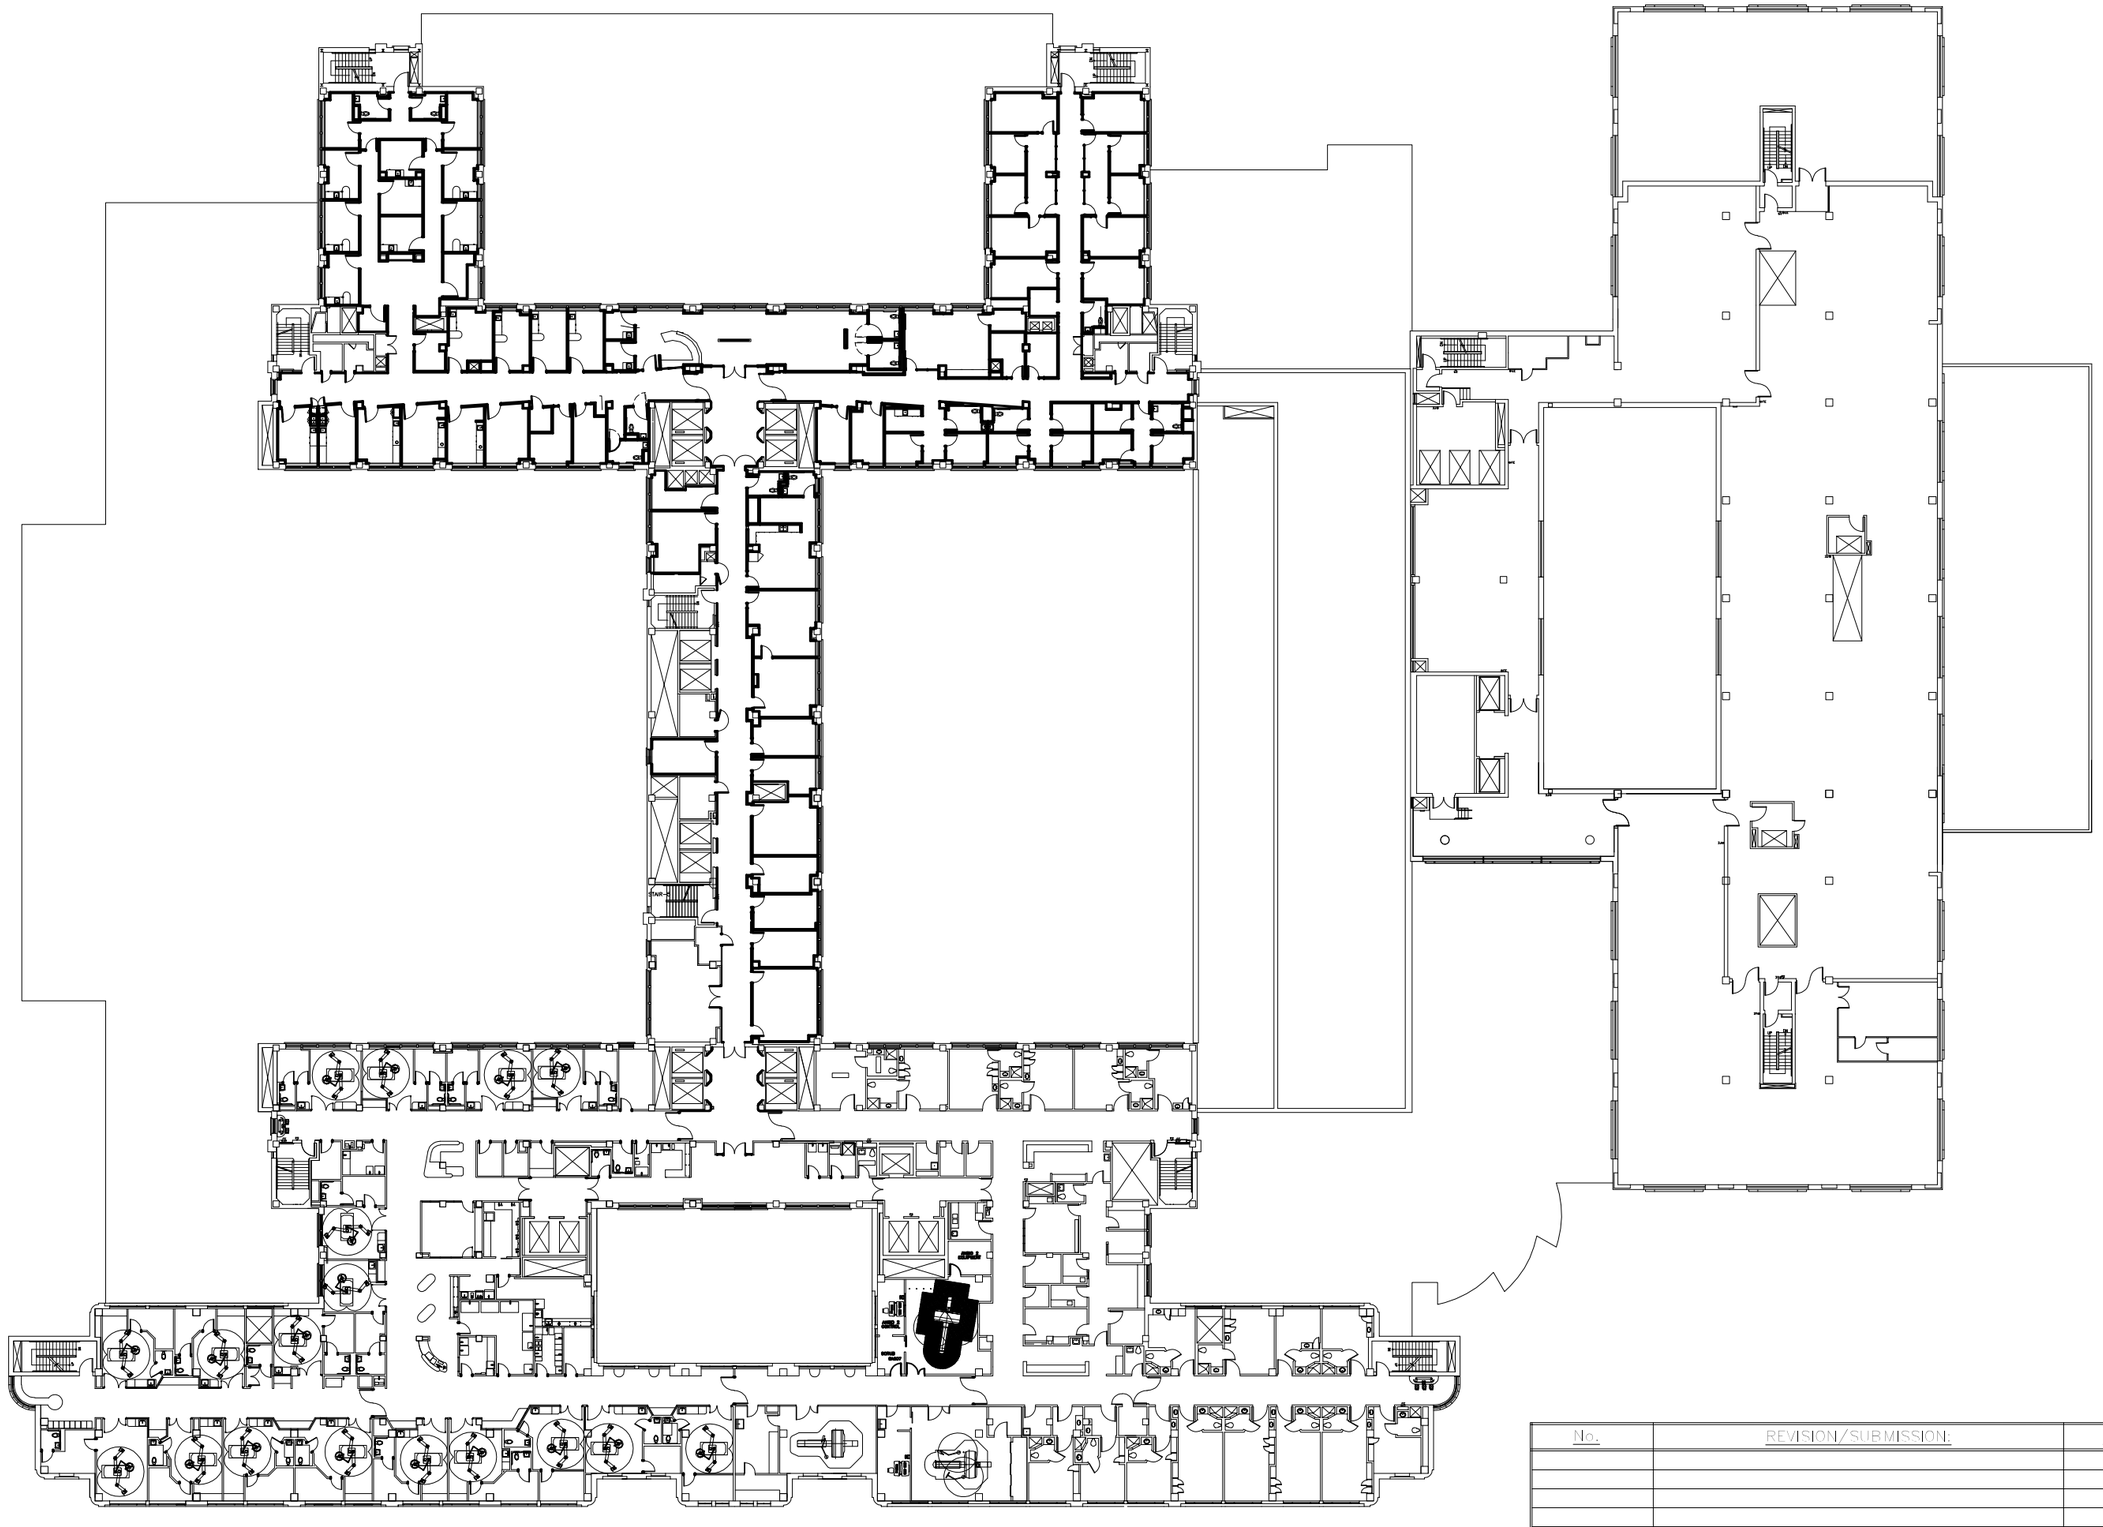

Grady
FACILITIES DEVELOPMENT

DEPARTMENT of FACILITIES MANAGEMENT
80 JESSE HILL, JR., DRIVE SE
ATLANTA, GEORGIA 30335
V: 404.616.4291
F: 404.616.3355

EIGHTH FLOOR PLANS

PROJECT NAME:
GRADY MEMORIAL HOSPITAL - BASE FLOOR PLANS


PROJECT LOCATION:
GRADY MEMORIAL HOSPITAL
80 JESSE HILL, JR., DRIVE SE
ATLANTA, GEORGIA 30303

No.	REVISION/SUBMISSION:	DATE:

PN: N/A
SCALE: NOT TO SCALE
DRAWN BY: gcs3
DATE: 5/9/2019

DRAWING TITLE: EIGHTH FLOOR
APPROVALS:
SHEET NUMBER: GMH-08

NOT FOR CONSTRUCTION

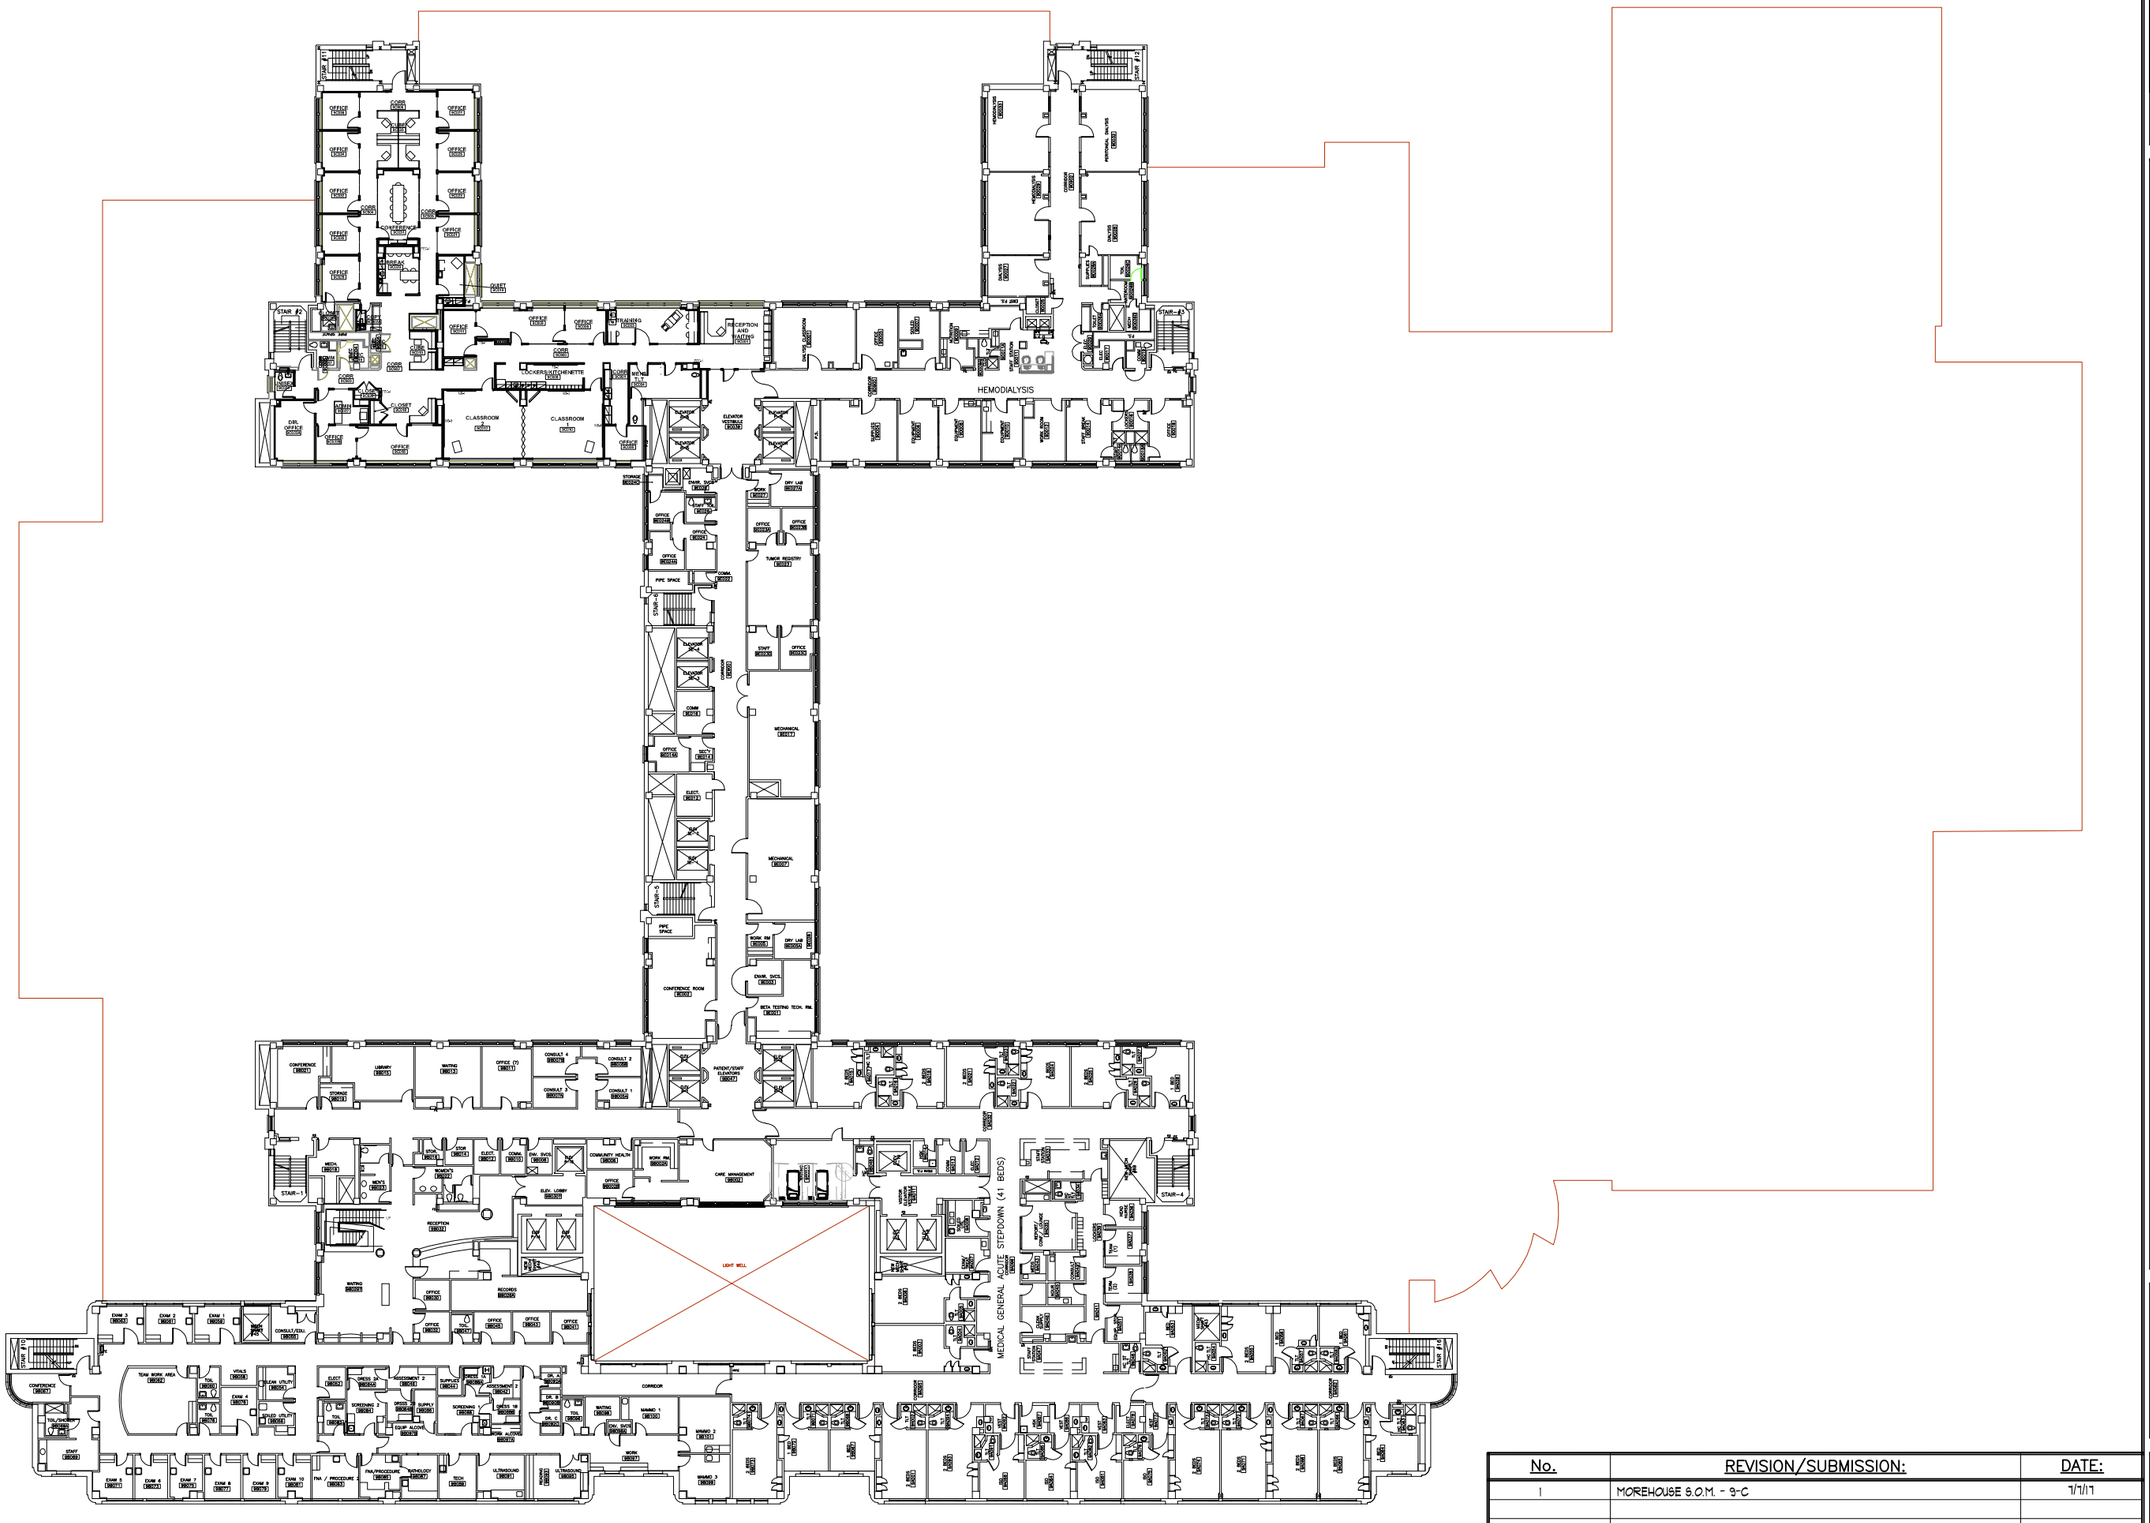

No.	REVISION/SUBMISSION:	DATE:
1	MOREHOUSE S.O.M. - 9-C	7/7/17

Grady
FACILITIES DEVELOPMENT

DEPARTMENT of FACILITIES MANAGEMENT
80 JESSE HILL, JR., DRIVE SE
ATLANTA, GEORGIA 30335
V: 404.616.4291
F: 404.616.3335


PROJECT NAME:
GRADY MEMORIAL HOSPITAL BASE PLANS

PROJECT LOCATION:
NINTH FLOOR
GRADY MEMORIAL HOSPITAL
ATLANTA, GEORGIA

PN: N/A
SCALE: NOT TO SCALE
DRAWN BY: gc53
DATE: 5/26/17

DRAWING TITLE: NINTH FLOOR
APPROVALS:
SHEET NUMBER: **GMH-09**

NOT FOR CONSTRUCTION

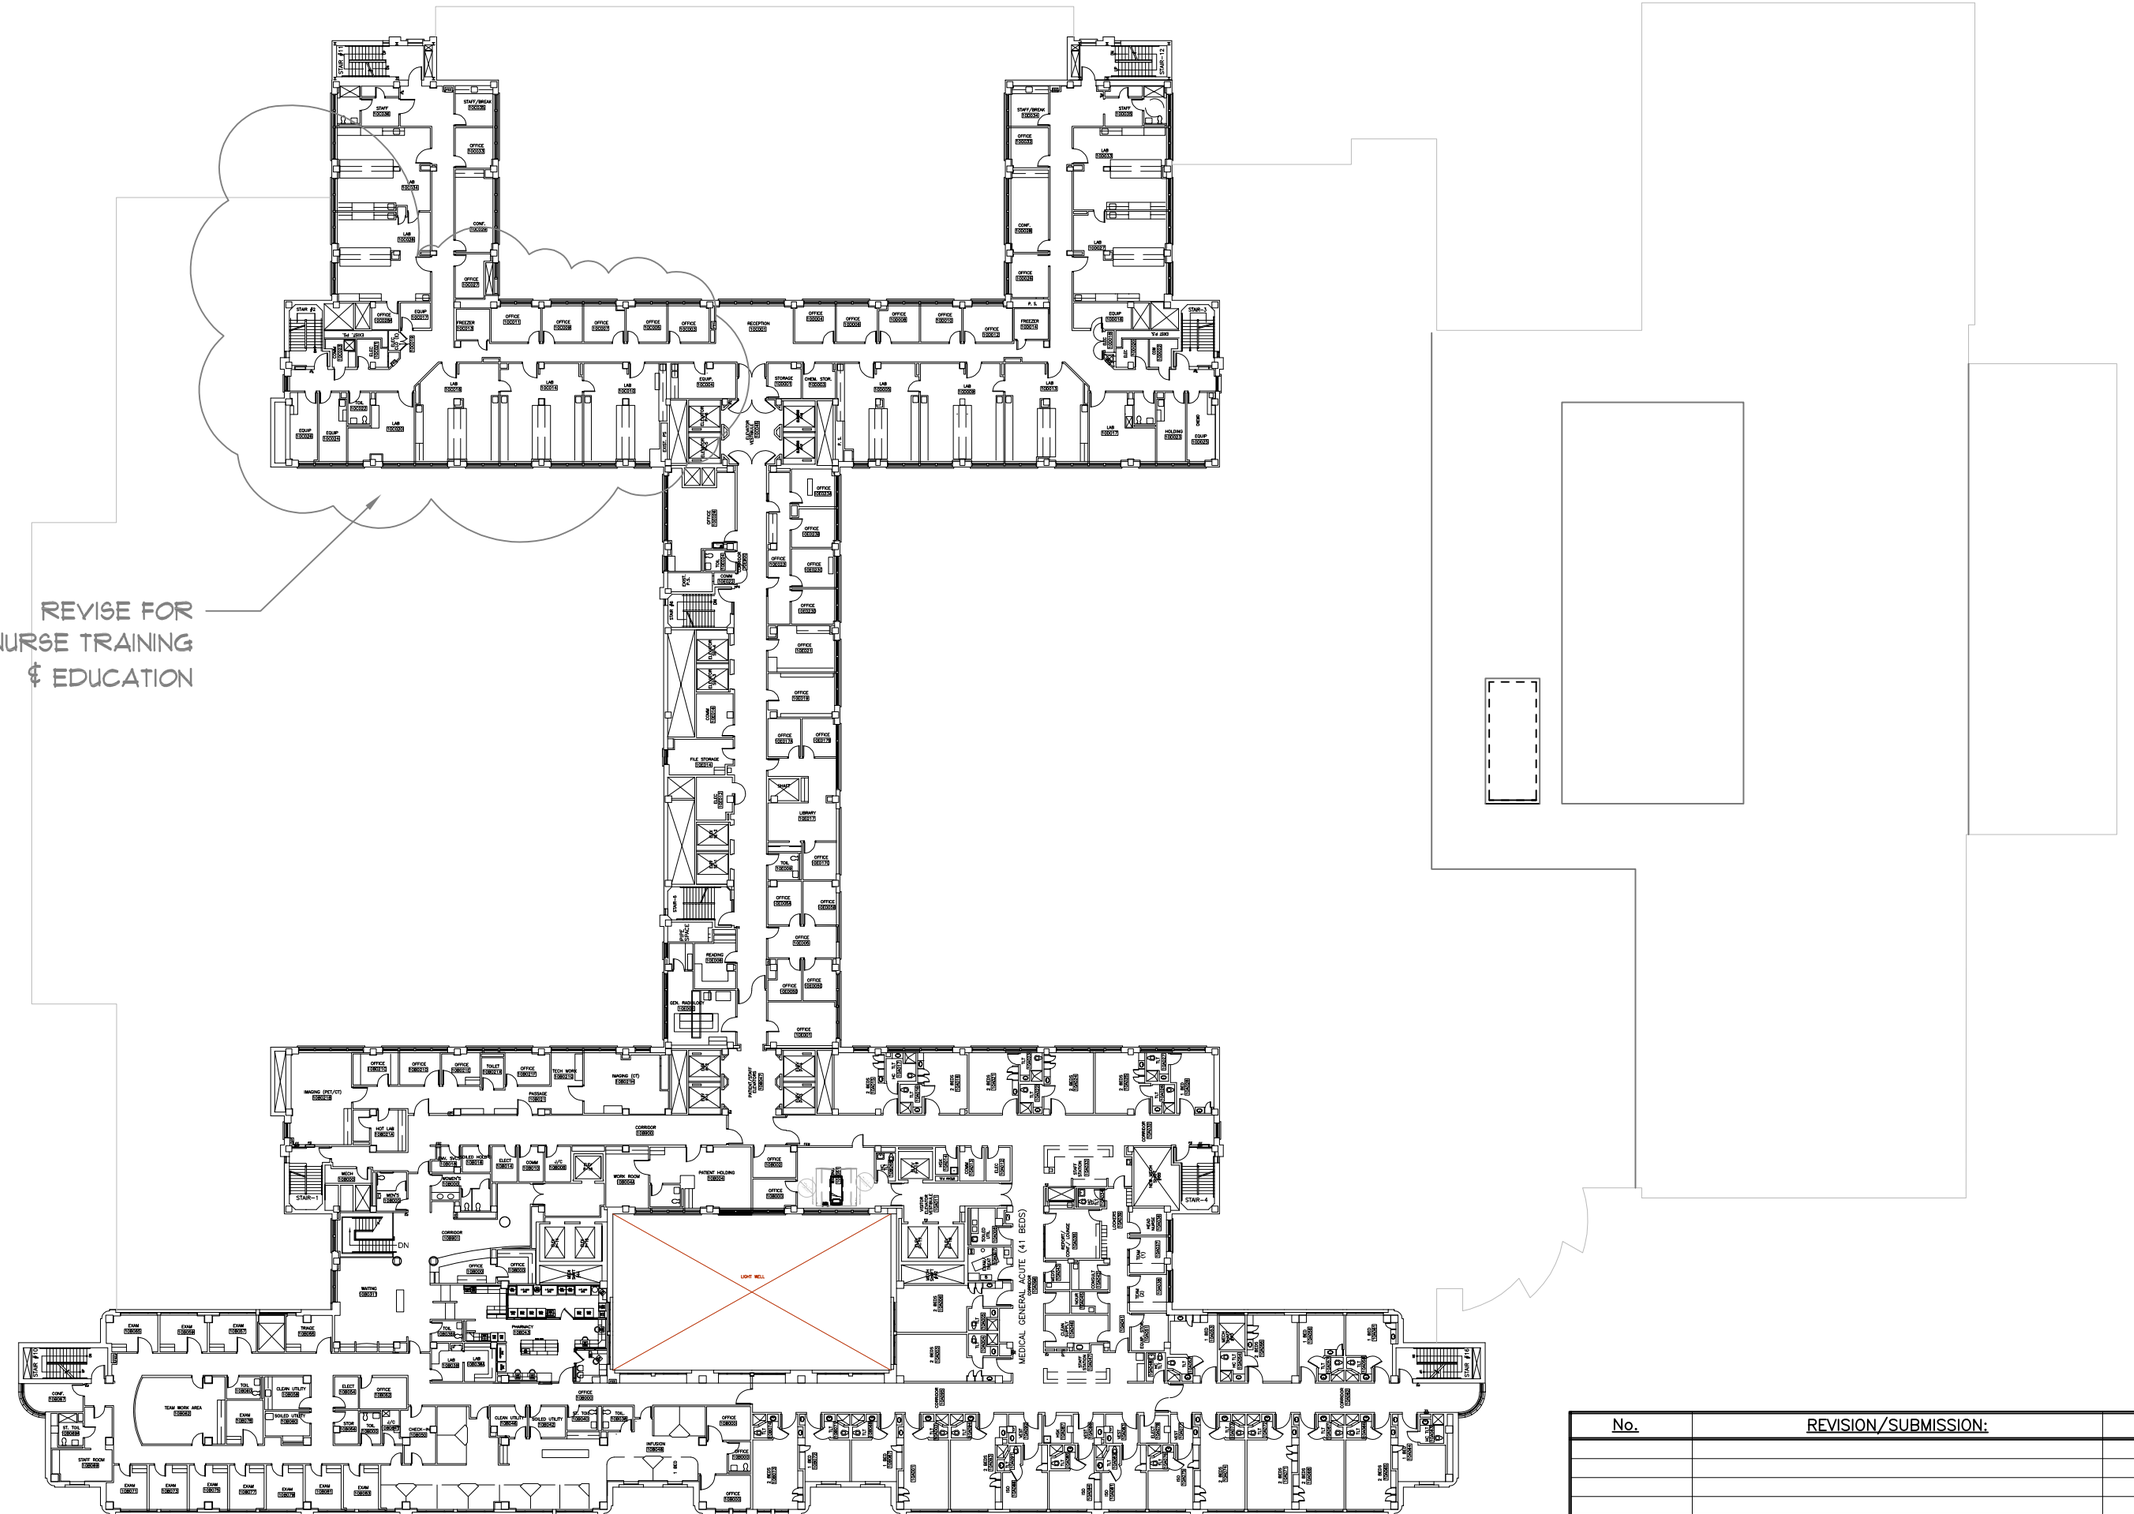

Grady
FACILITIES DEVELOPMENT
DEPARTMENT of FACILITIES MANAGEMENT
80 JESSE HILL, JR., DRIVE SE
ATLANTA, GEORGIA 30335
V: 404.616.4291
F: 404.616.3335

PROJECT NAME:
GRADY MEMORIAL HOSPITAL BASE PLANS


PROJECT LOCATION:
TENTH FLOOR
80 JESSE HILL, JR., DRIVE SE
ATLANTA, GEORGIA 30303

PN:	N/A
SCALE:	NOT TO SCALE
DRAWN BY:	gcs3
DATE:	5/26/17

No.	REVISION/SUBMISSION:	DATE:

DRAWING TITLE: TENTH FLOOR
APPROVALS:
SHEET NUMBER: **GMH-10**

NOT FOR CONSTRUCTION

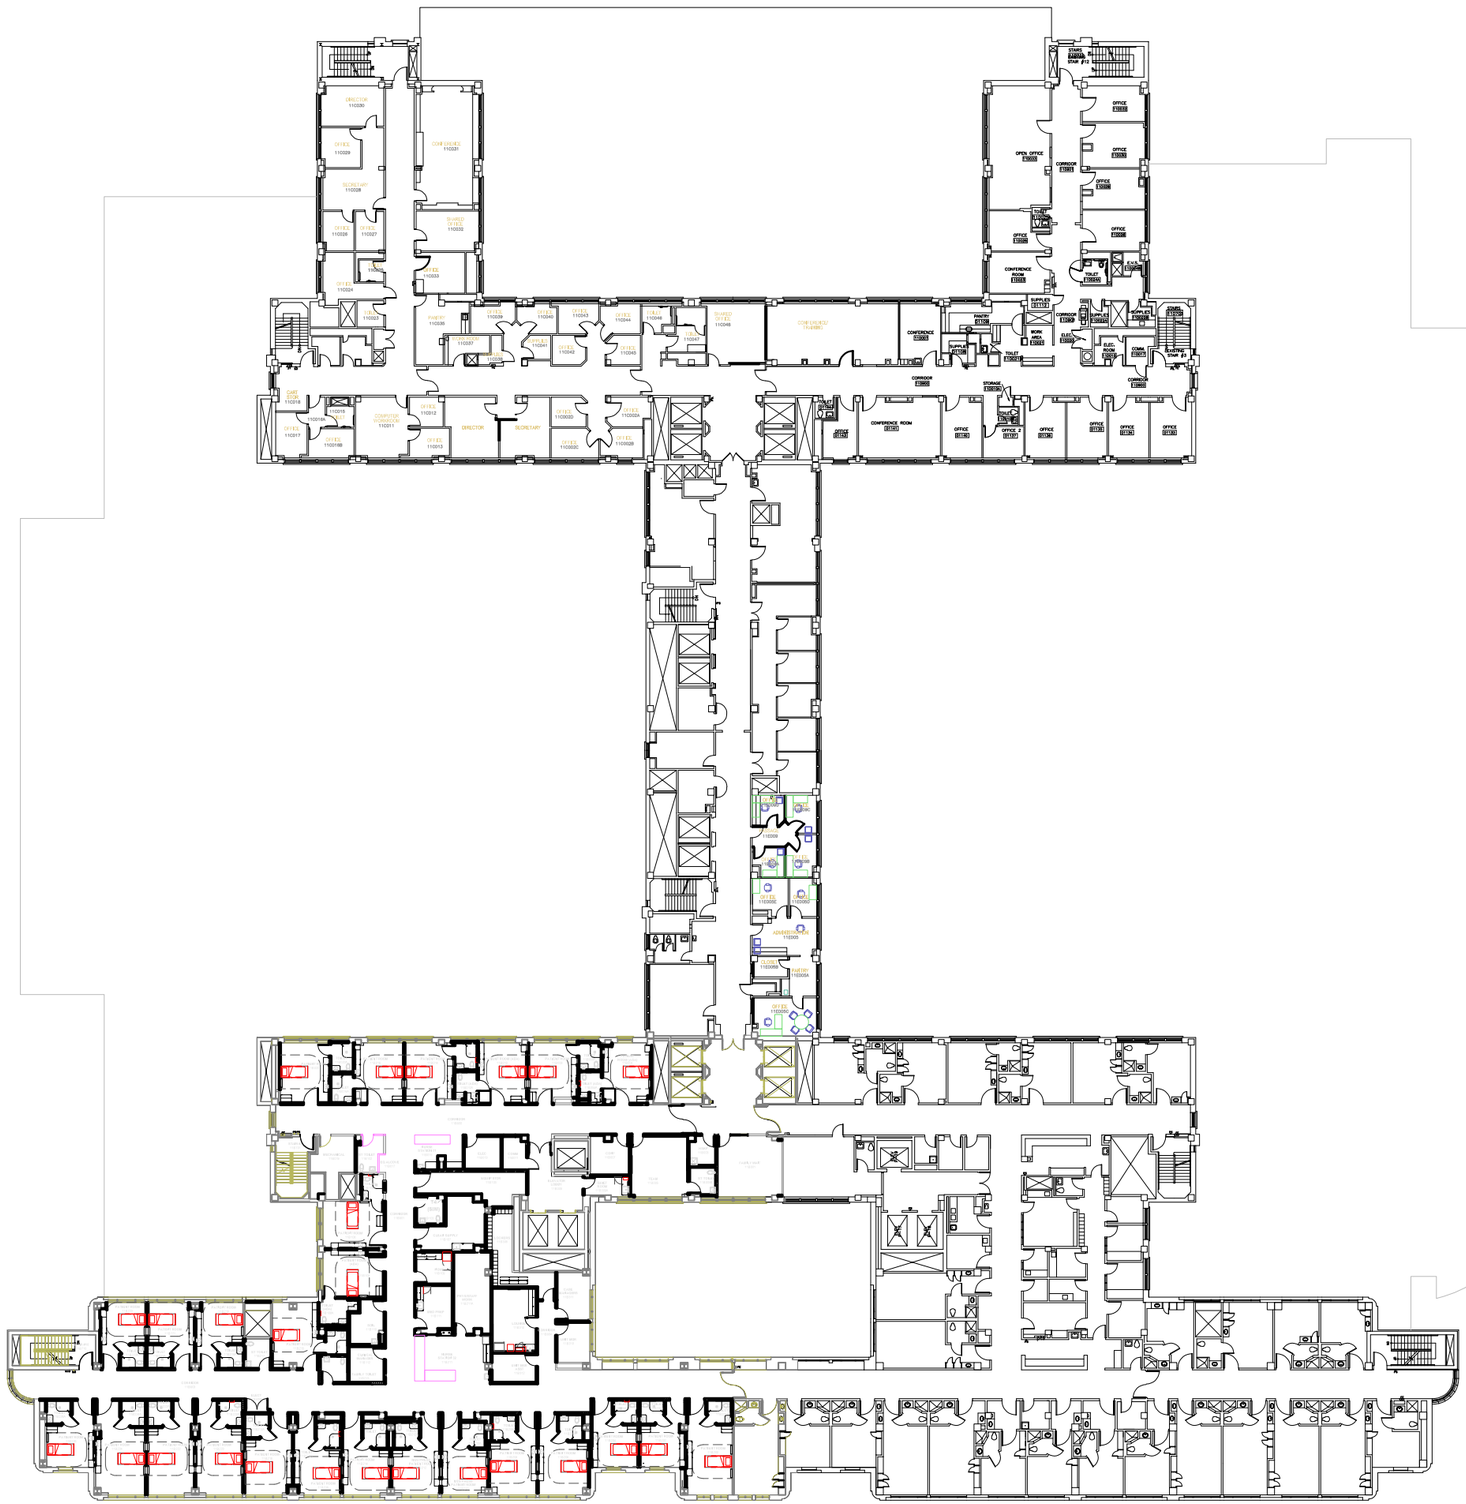

Grady
FACILITIES DEVELOPMENT

DEPARTMENT of FACILITIES MANAGEMENT
80 JESSE HILL, JR., DRIVE SE
ATLANTA, GEORGIA 30335
V: 404.616.4291
F: 404.616.3355

PROJECT NAME:
GRADY MEMORIAL HOSPITAL - BASE PLANS


PROJECT LOCATION:
ELEVENTH FLOOR
80 JESSE HILL, JR., DRIVE SE
ATLANTA, GEORGIA 30303

No.	REVISION/SUBMISSION:	DATE:
1	11-B MED-SURG REMODELING	9/27/18

PN: N/A
SCALE: NOT TO SCALE
DRAWN BY: gcs3
DATE: 3/30/11

DRAWING TITLE: ELEVENTH FLOOR
APPROVALS:
SHEET NUMBER: GMH-11

NOT FOR CONSTRUCTION

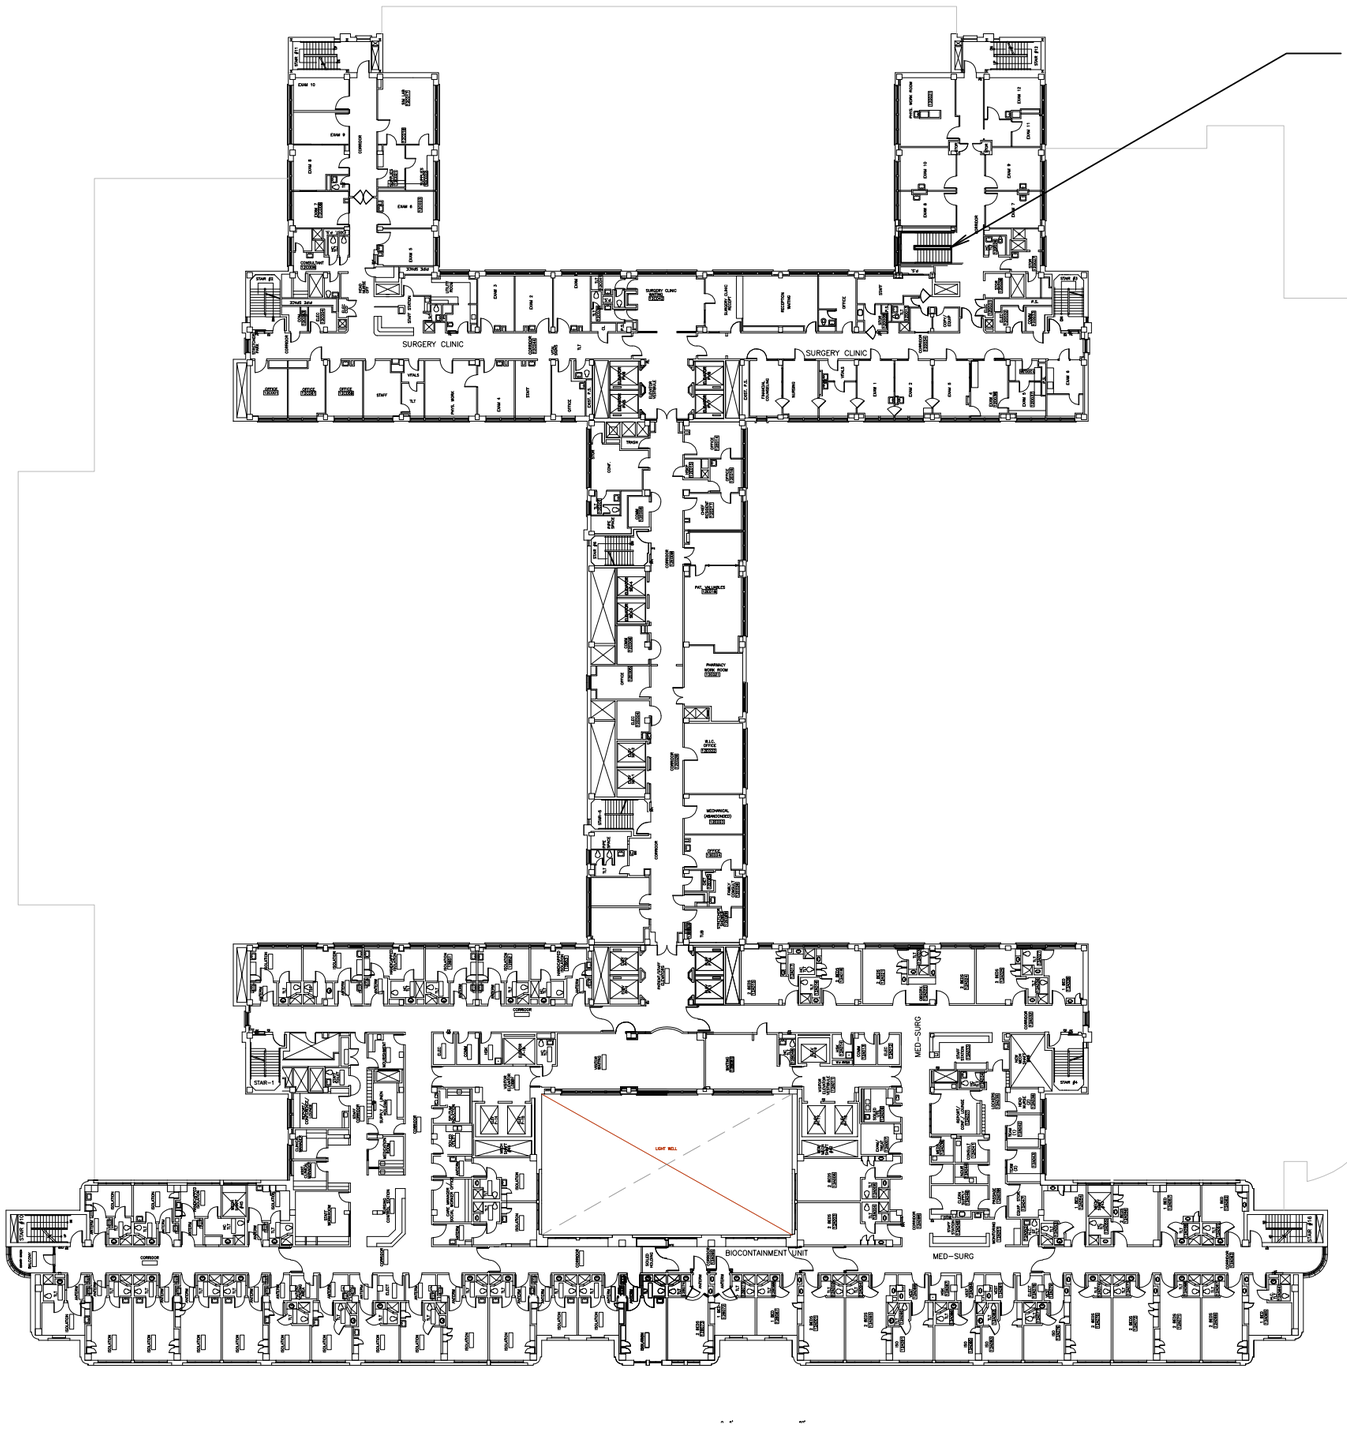

Grady
FACILITIES DEVELOPMENT
DEPARTMENT of FACILITIES MANAGEMENT
80 JESSE HILL, JR., DRIVE SE
ATLANTA, GEORGIA 30335
V: 404.616.4291
F: 404.616.3335

PROJECT NAME:
GRADY MEMORIAL HOSPITAL BASE PLANS


PROJECT LOCATION:
TWELFTH FLOOR
80 JESSE HILL, JR., DRIVE SE
ATLANTA, GEORGIA 30303

PN:	N/A
SCALE:	N.T.S.
DRAWN BY:	gcs3
DATE:	3/30/11

No.	REVISION/SUBMISSION:	DATE:

DRAWING TITLE:	TWELFTH FLOOR
APPROVALS:	
SHEET NUMBER:	GMH-12-C

NOT FOR CONSTRUCTION

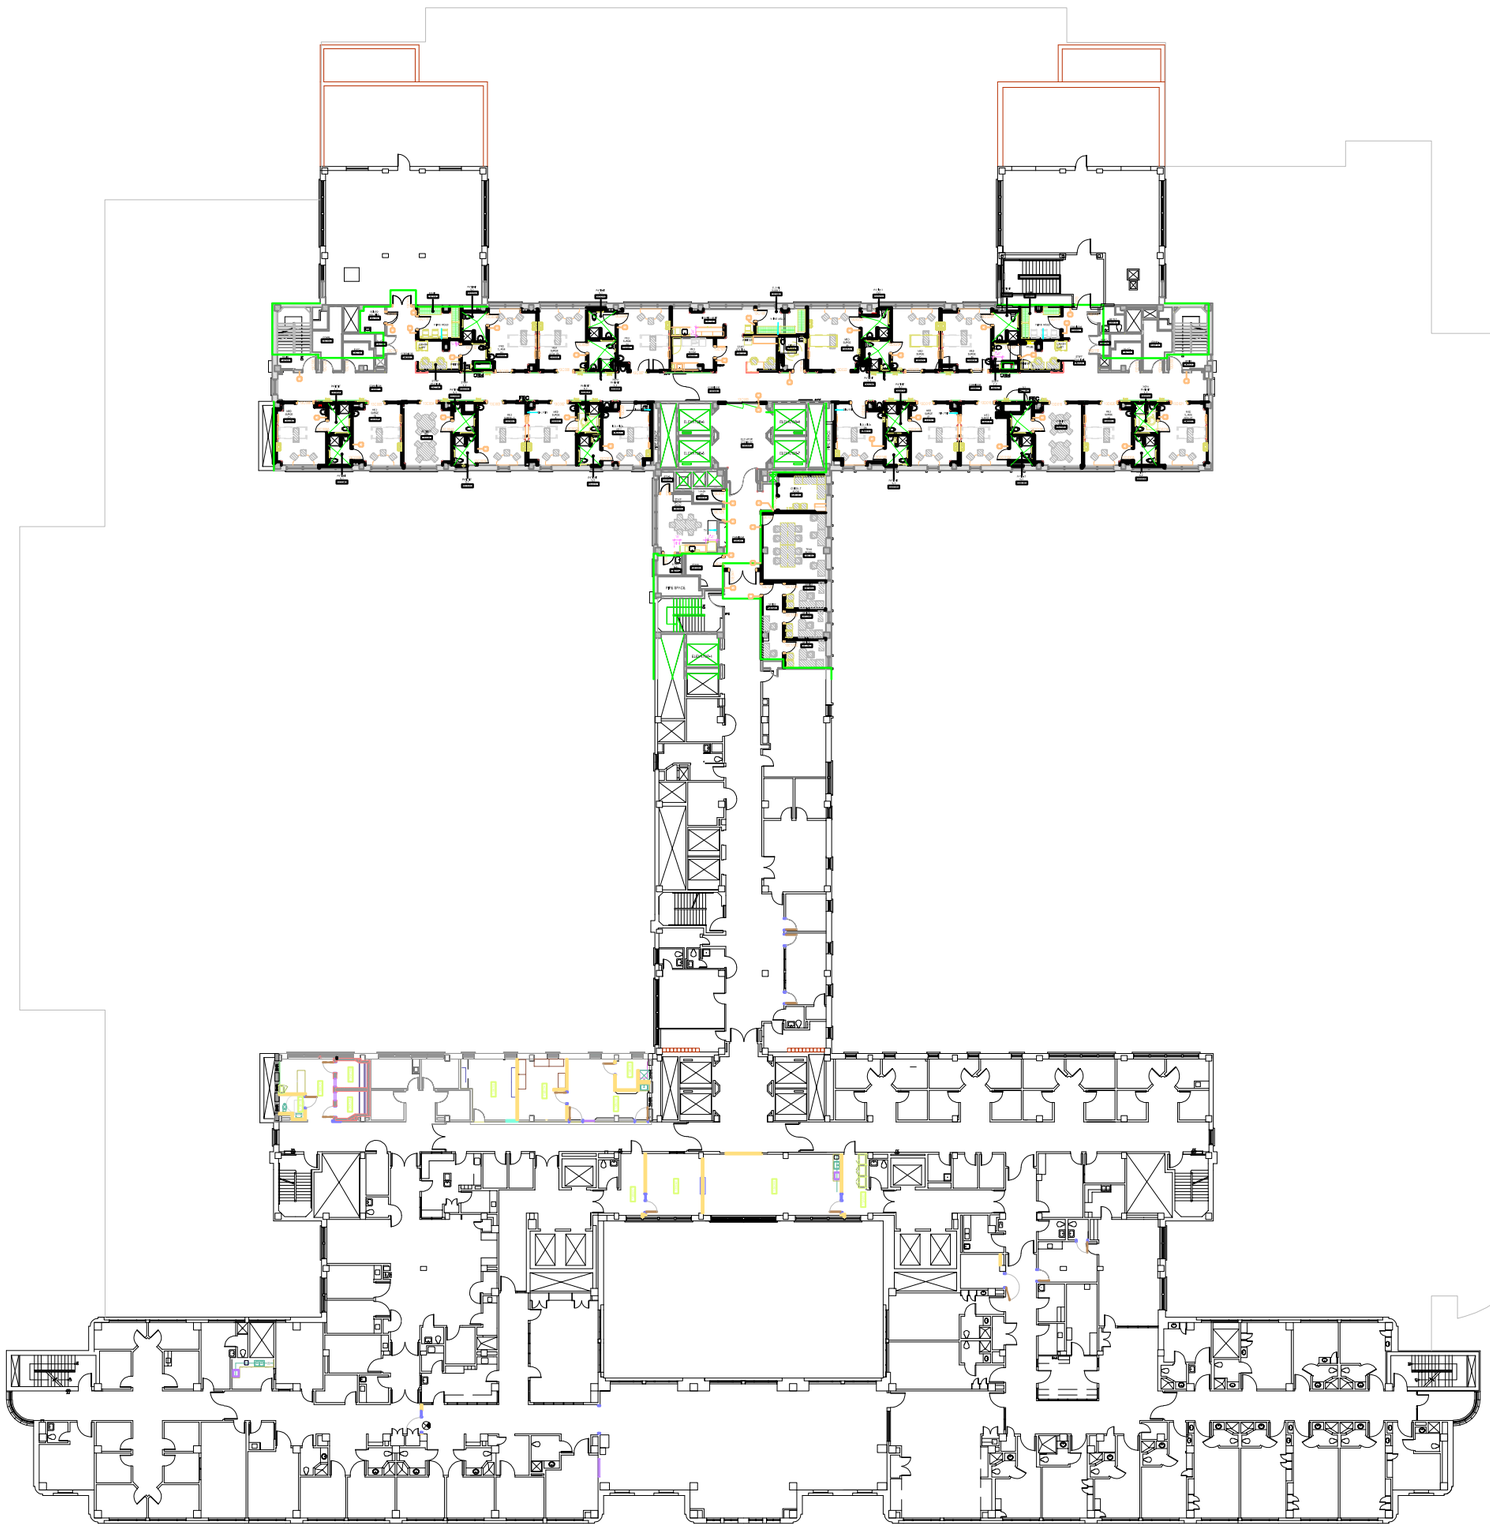

Grady
FACILITIES DEVELOPMENT

DEPARTMENT of FACILITIES MANAGEMENT
80 JESSE HILL, JR., DRIVE SE
ATLANTA, GEORGIA 30335
V: 404.616.4291
F: 404.616.3355

PROJECT NAME:
GRADY MEMORIAL HOSPITAL BASE PLANS


PROJECT LOCATION:
THIRTEENTH FLOOR
80 JESSE HILL, JR., DRIVE SE
ATLANTA, GEORGIA 30303

PN:	11226
SCALE:	N.T.S.
DRAWN BY:	gcs3
DATE:	3/30/11

DRAWING TITLE:	THIRTEENTH FLOOR
APPROVALS:	
SHEET NUMBER:	GMH-13

NOT FOR CONSTRUCTION

No.	REVISION/SUBMISSION:	DATE:
1	C & D MED-SURG REMODELING	1/26/22

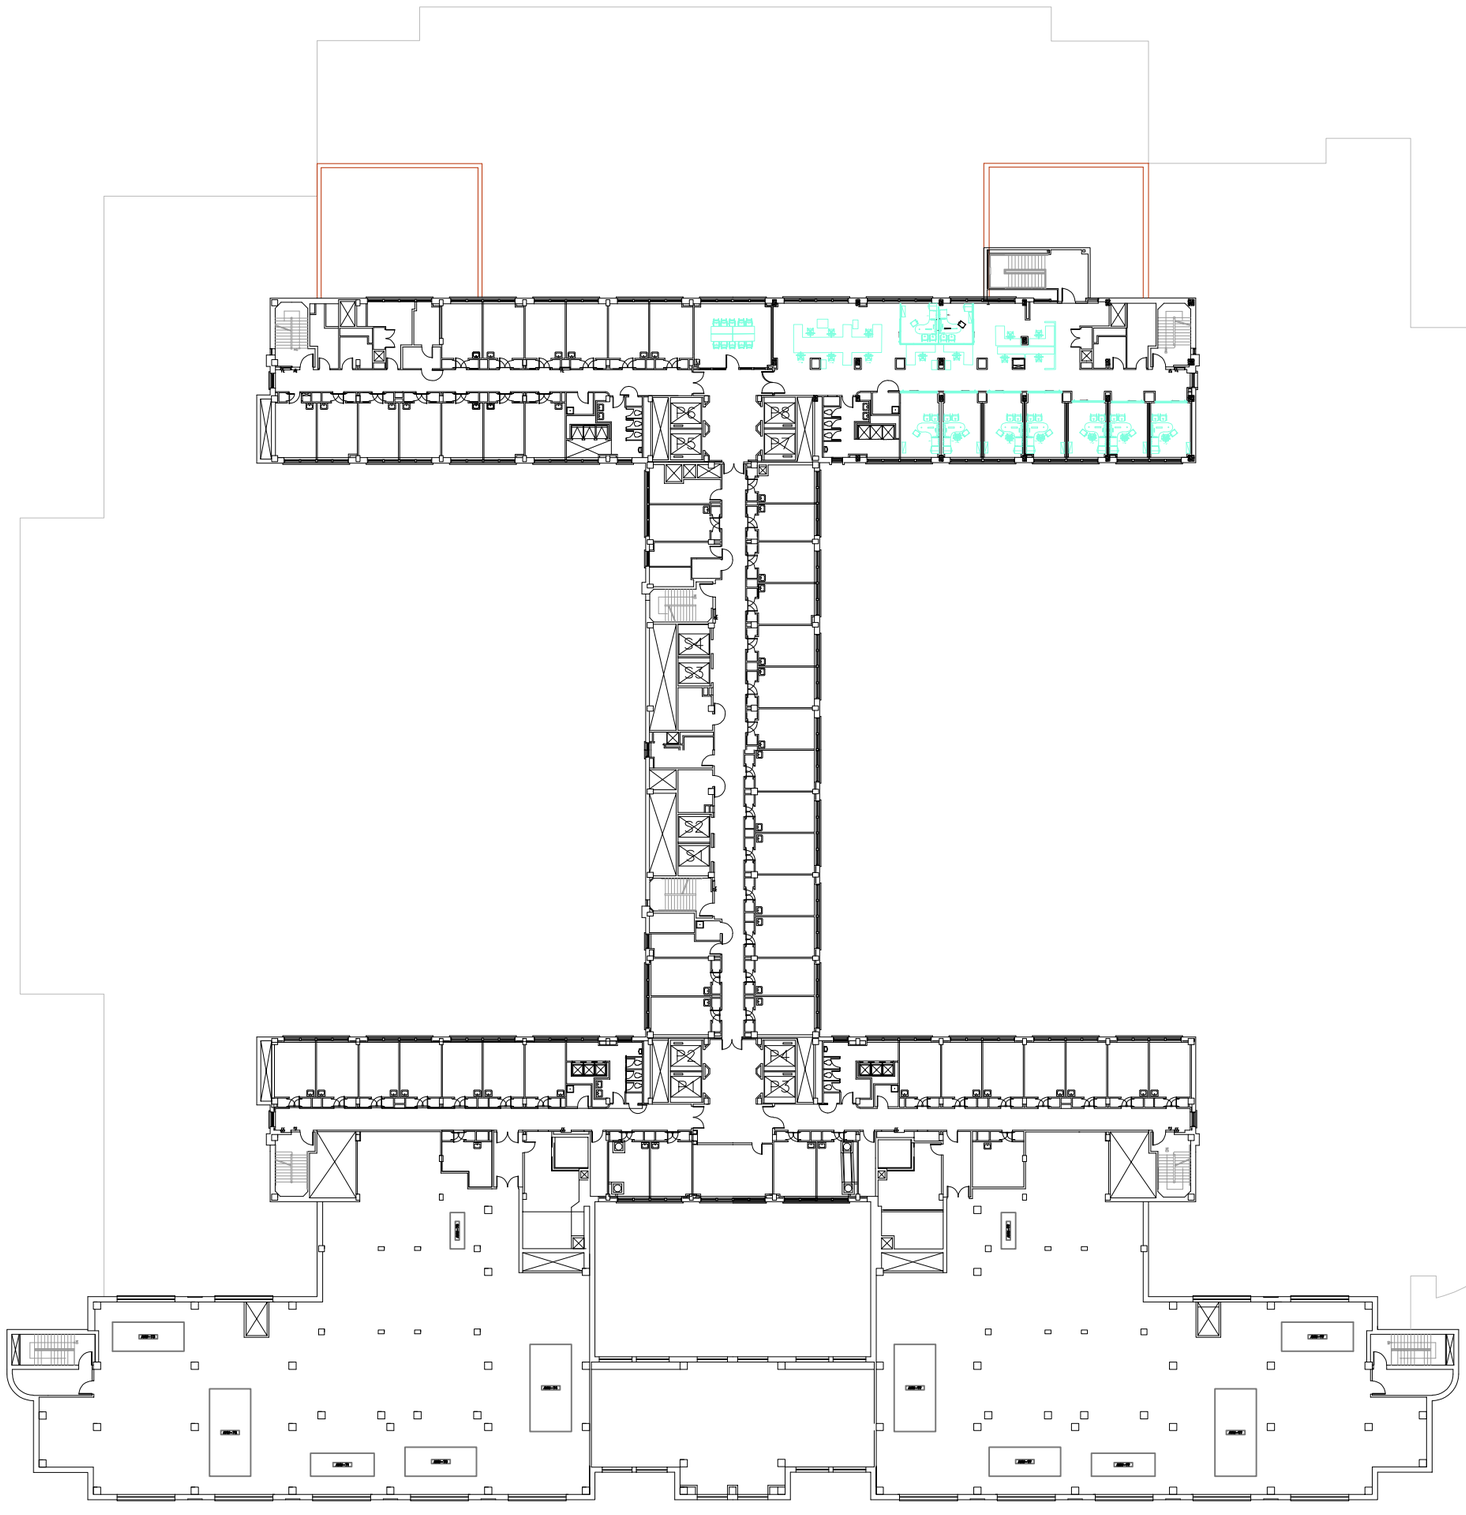

Grady
FACILITIES DEVELOPMENT

DEPARTMENT of FACILITIES MANAGEMENT
80 JESSE HILL, JR., DRIVE SE
ATLANTA, GEORGIA 30335
V: 404.616.4291
F: 404.616.3335

PROJECT NAME:
GRADY MEMORIAL HOSPITAL BASE PLANS


PROJECT LOCATION:
FOURTEENTH FLOOR
80 JESSE HILL, JR., DRIVE SE
ATLANTA, GEORGIA 30303

PN:	N/A
SCALE:	NOT TO SCALE
DRAWN BY:	gcs3
DATE:	3/30/11

No.	REVISION/SUBMISSION:	DATE:
1	14-D INFRASTRUCTURE & EXIST STAIR	1/25/22

DRAWING TITLE:	FOURTEENTH FLOOR
APPROVALS:	
SHEET NUMBER:	GMH-14

NOT FOR CONSTRUCTION

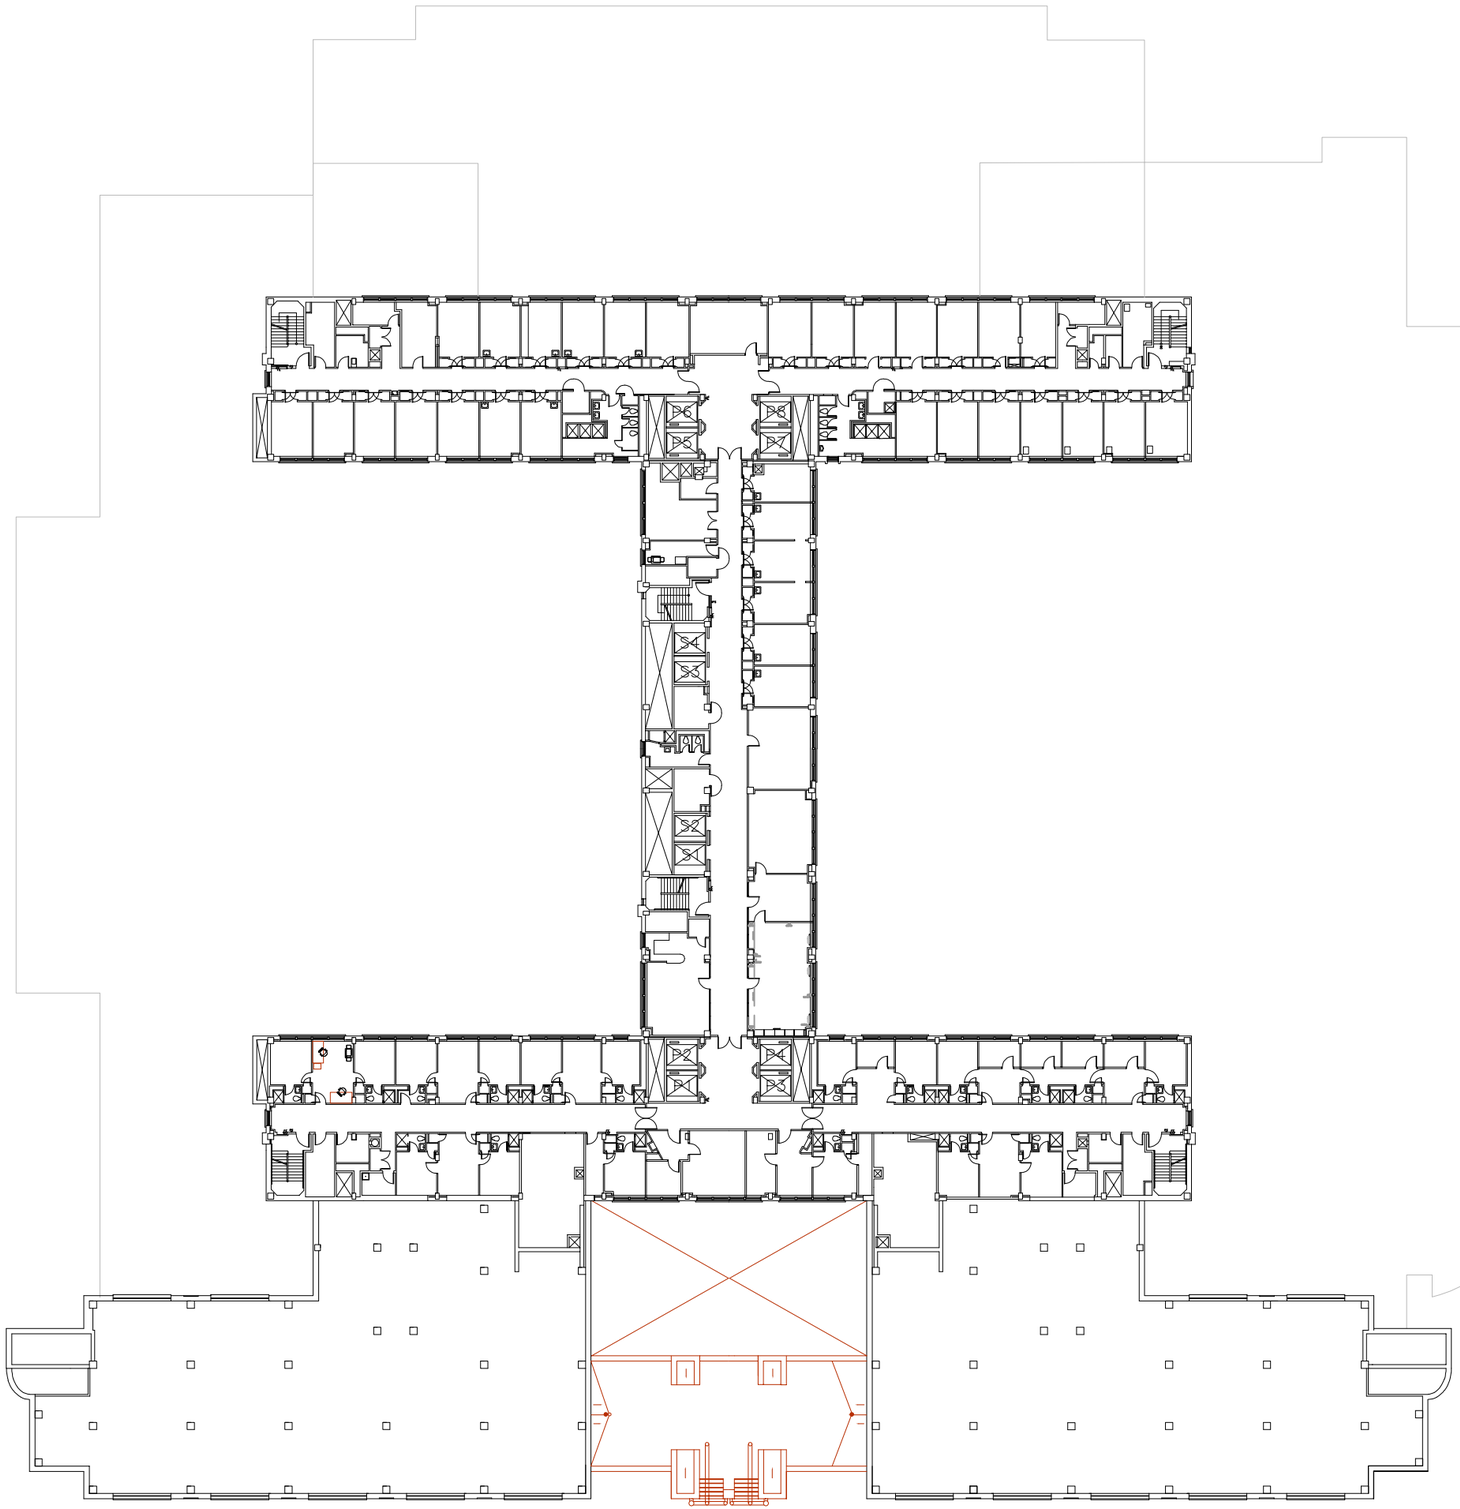

Grady

DEPARTMENT of FACILITIES MANAGEMENT
80 JESSE HILL, JR., DRIVE SE
ATLANTA, GEORGIA 30335
V: 404.616.4291
F: 404.616.3355

PROJECT NAME:
GRADY MEMORIAL HOSPITAL – BASE PLANS


PROJECT LOCATION:
FIFTEENTH FLOOR
80 JESSE HILL, JR., DRIVE SE
ATLANTA, GEORGIA 30303

PN:	N/A
SCALE:	NOT TO SCALE
DRAWN BY:	gcs3
DATE:	3/30/11

No.	REVISION/SUBMISSION:	DATE:

DRAWING TITLE:	FIFTEENTH FLOOR
APPROVALS:	
SHEET NUMBER:	GMH-15

NOT FOR CONSTRUCTION

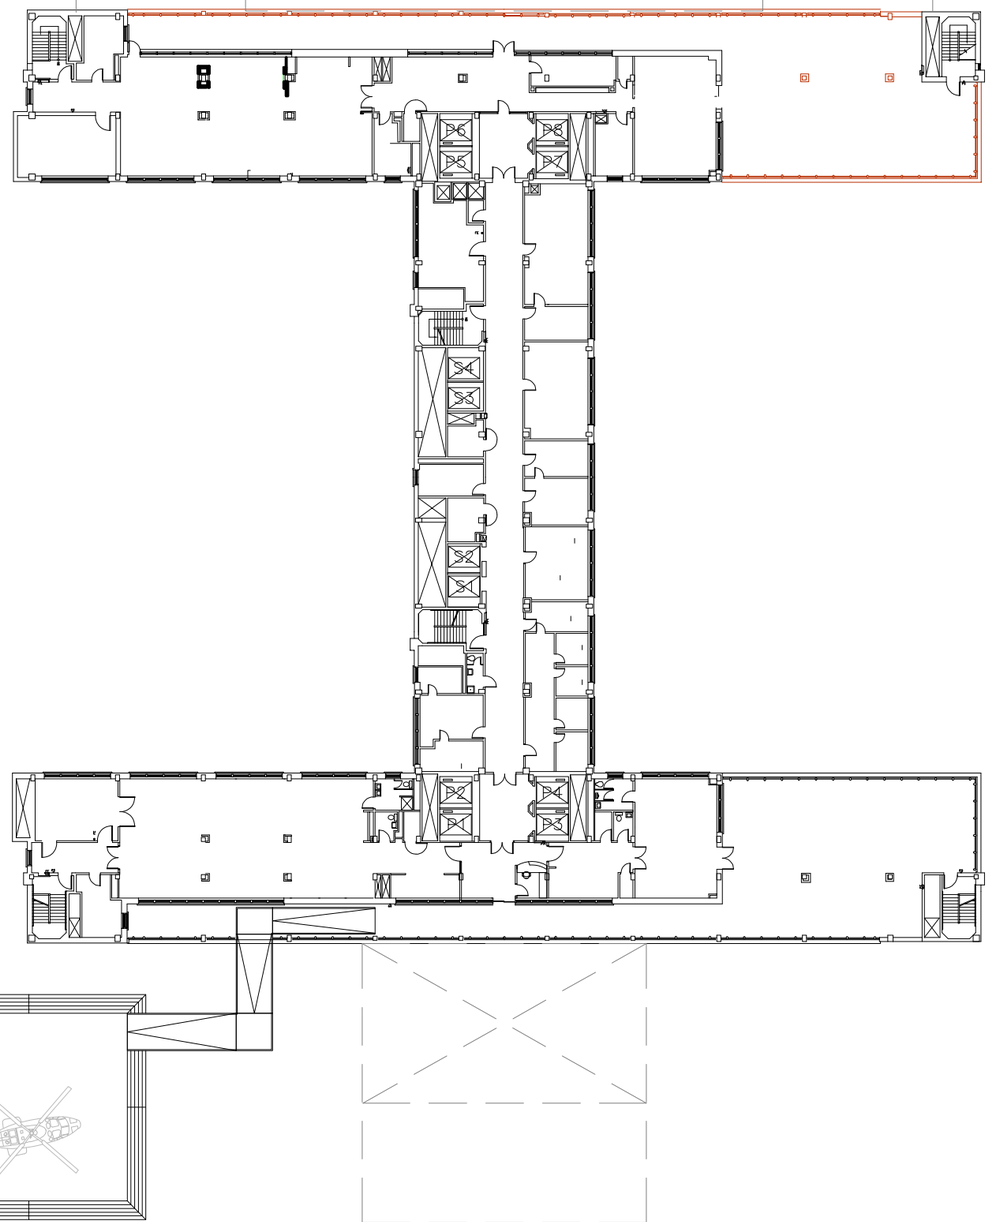

Grady
FACILITIES DEVELOPMENT
DEPARTMENT of FACILITIES MANAGEMENT
80 JESSE HILL, JR., DRIVE SE
ATLANTA, GEORGIA 30335
V: 404.616.4291
F: 404.616.3355

PROJECT NAME:
GRADY BASE PLANS


PROJECT LOCATION:
GRADY MEMORIAL HOSPITAL
80 JESSE HILL, JR., DRIVE SE
ATLANTA, GEORGIA 30303

PN:	N/A
SCALE:	NTS
DRAWN BY:	gc53
DATE:	3/30/11


No.	REVISION/SUBMISSION:	DATE:
1	RESIDENT RESOURCE CENTER REMODELING	2/17/22

DRAWING TITLE: FLOOR PLAN
APPROVALS:
SHEET NUMBER: GMH-16


NOT FOR CONSTRUCTION

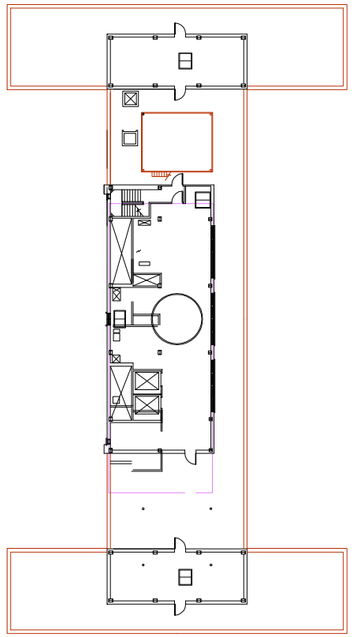


EIGHTEENTH FLOOR PLAN

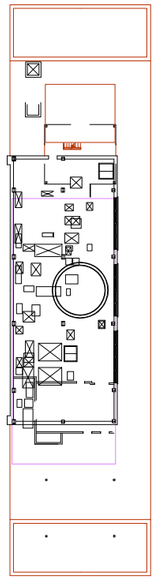


NINETEENTH FLOOR PLAN

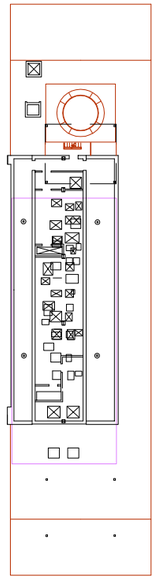


TWENTIETH FLOOR PLAN

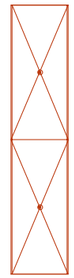

TWENTIETH FLOOR / ROOF PLAN

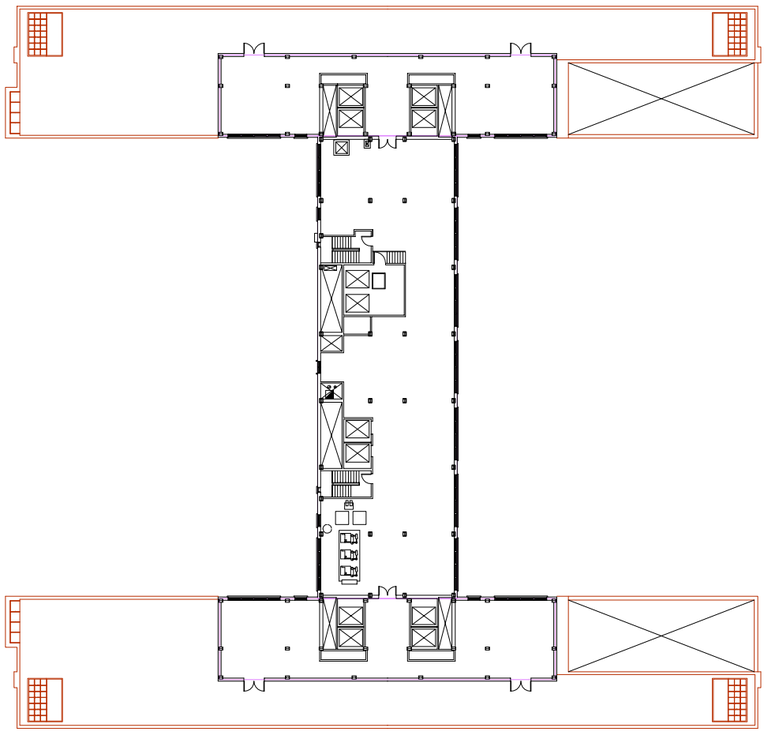

SEVENTEENTH FLOOR PLAN

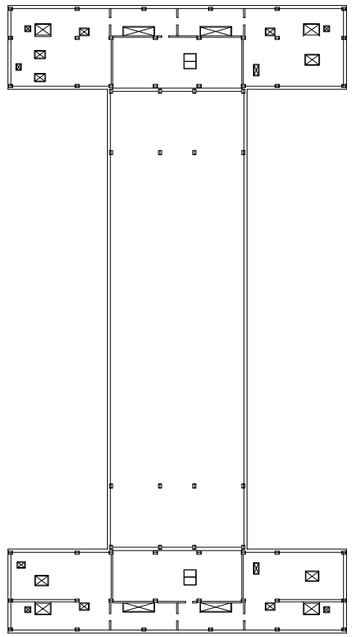

SEVENTEENTH FLOOR – PLENUM

No.	REVISION/SUBMISSION:	DATE:

Grady
FACILITIES DEVELOPMENT
DEPARTMENT of FACILITIES MANAGEMENT
80 JESSE HILL, JR., DRIVE SE
ATLANTA, GEORGIA 30335
V: 404.616.4291
F: 404.616.3355

PROJECT NAME:
GRADY BASE PLANS

PROJECT LOCATION:
GRADY MEMORIAL HOSPITAL
80 JESSE HILL, JR., DRIVE SE
ATLANTA, GEORGIA 30303

PN: N/A
SCALE: NOT TO SCALE
DRAWN BY: gc53
DATE: 3/30/11

DRAWING TITLE: PENTHOUSE
APPROVALS:
SHEET NUMBER: GMH-MP

NOT FOR CONSTRUCTION